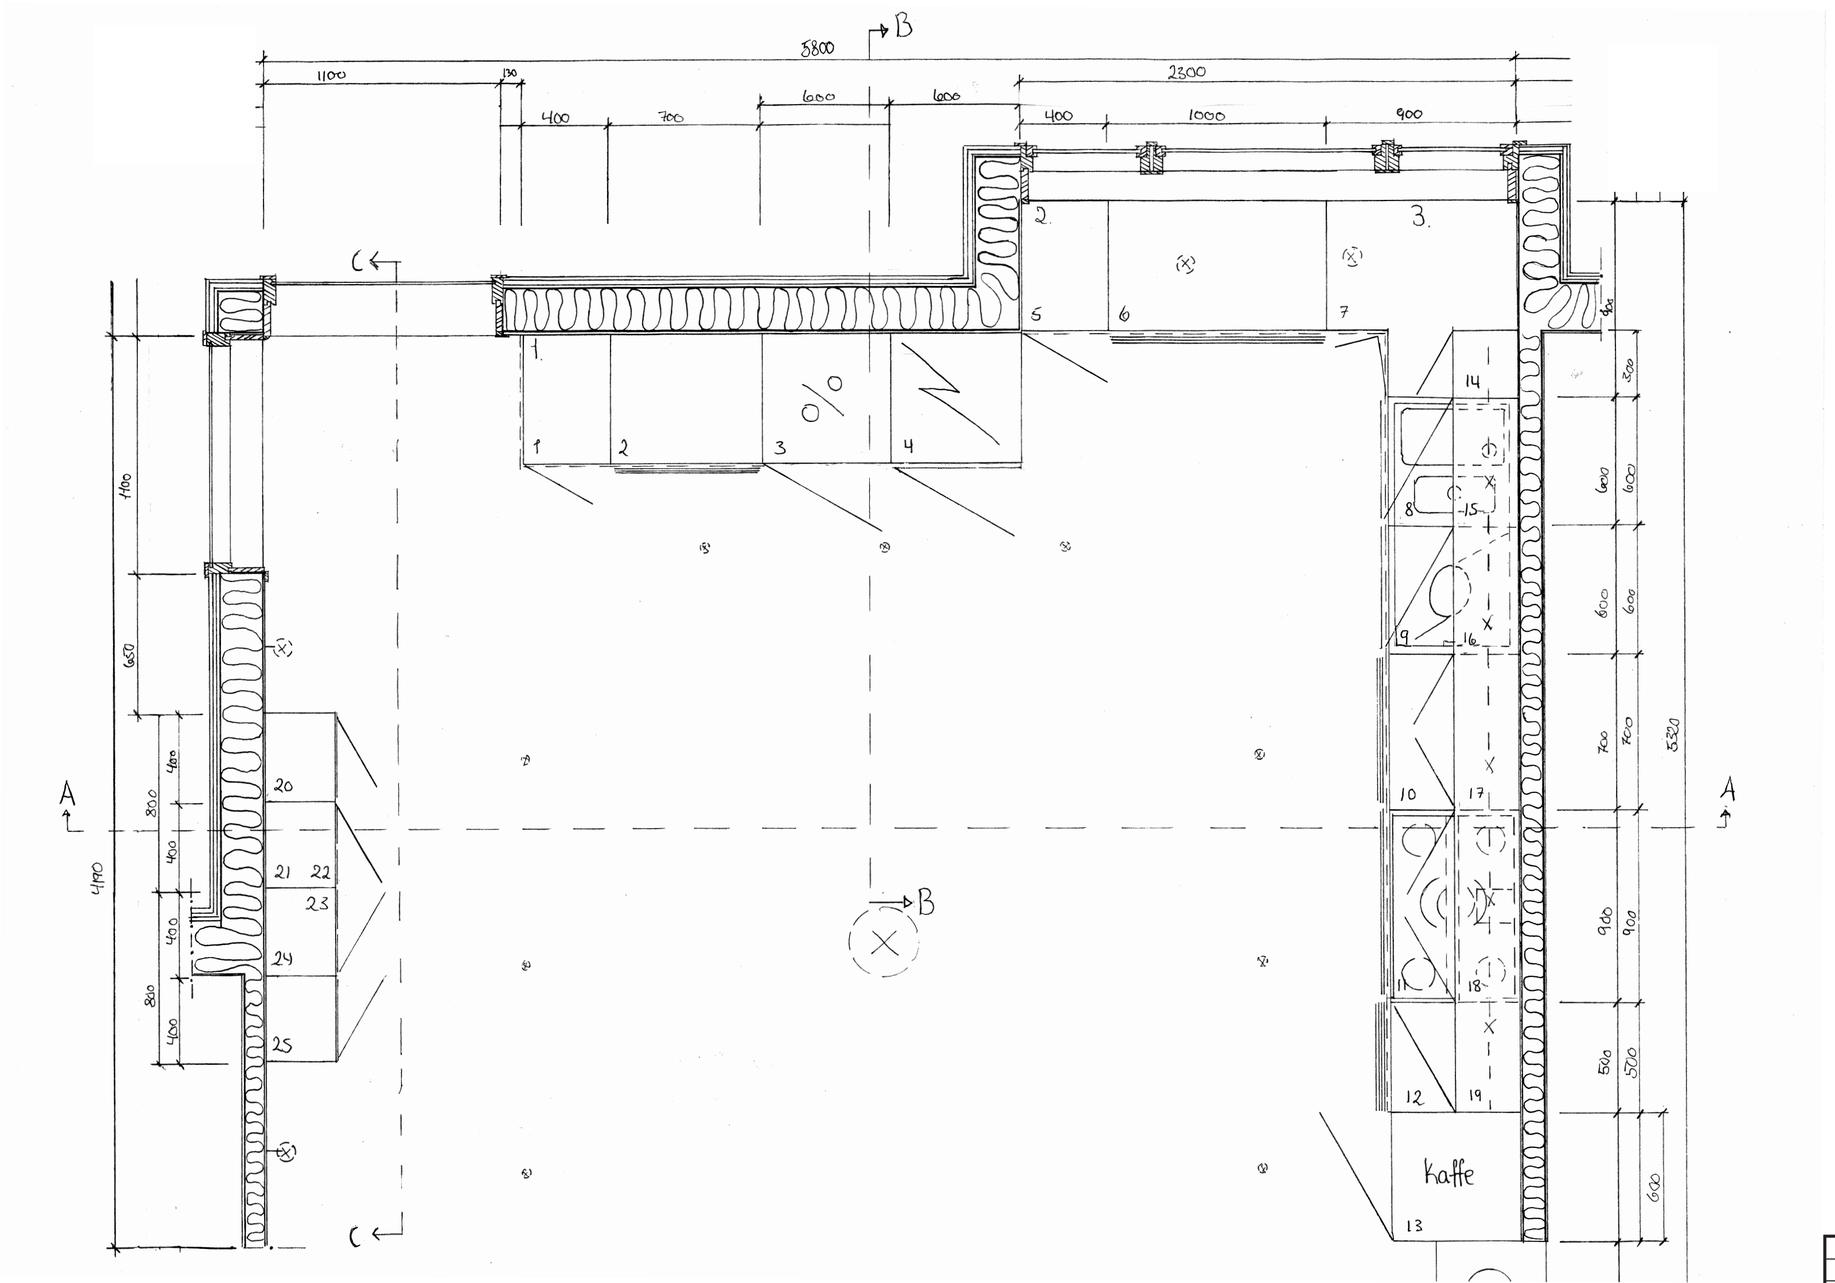
B
5800
1100
130
400
700
600
600
2300
400
1000
900
C
A
1400
650
800
400
400
400
400
4400
300
600
600
600
600
700
700
5320
900
900
500
500
600
Kaffe

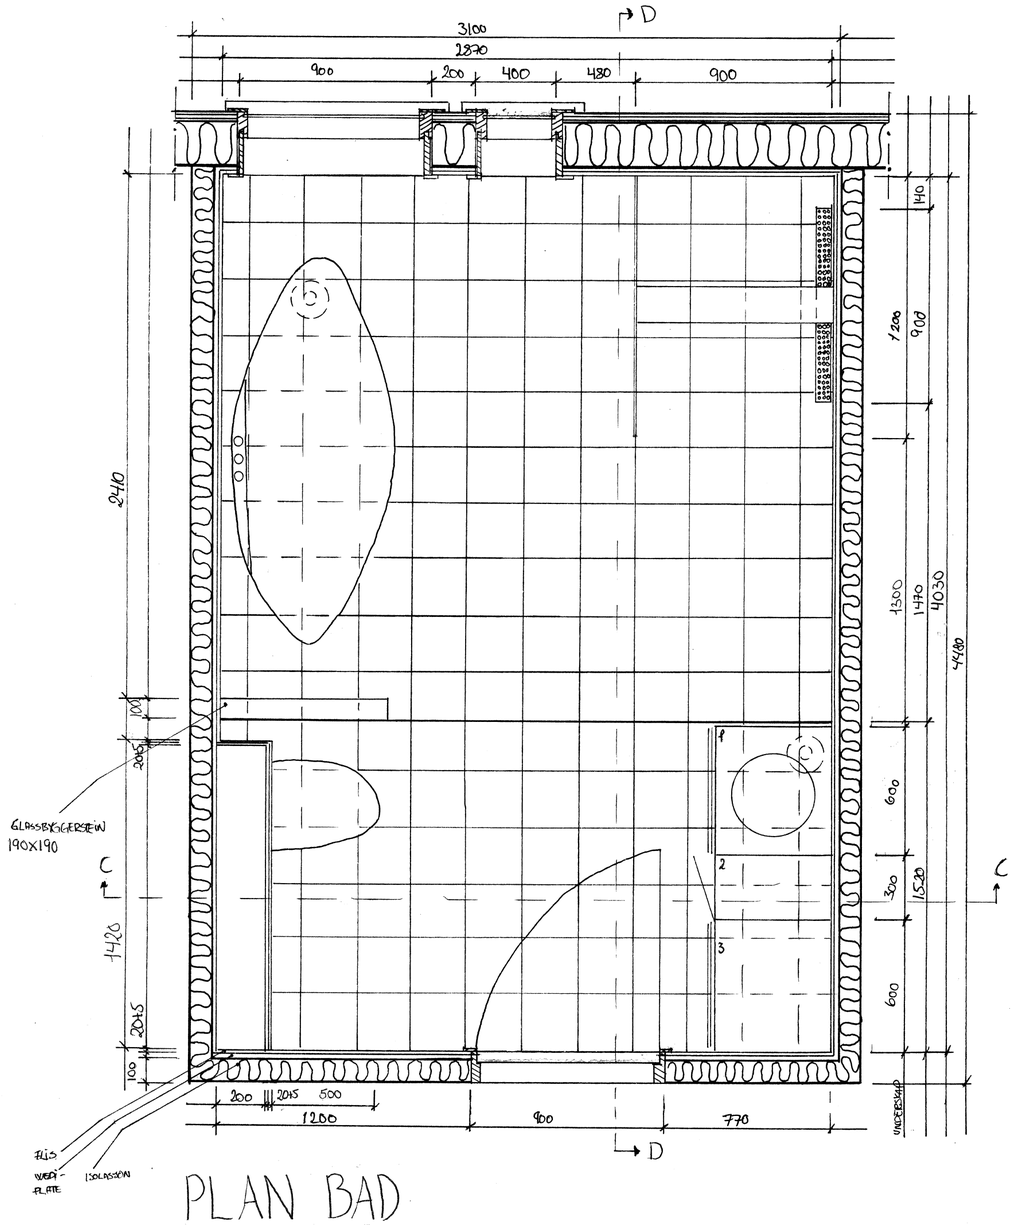
D
3100
2870
900
200
400
430
900
110
1200
900
1300
1470
4030
4480
2470
100
2015
GLASSBYGGERSTEIN
190x190
C
1420
2015
100
200
2015
500
1200
900
770
D
FLIS
VATT-
PLATTE
ISOLASJON
1
2
3
600
300
1520
600
UNDERSKAP

PLAN BAD

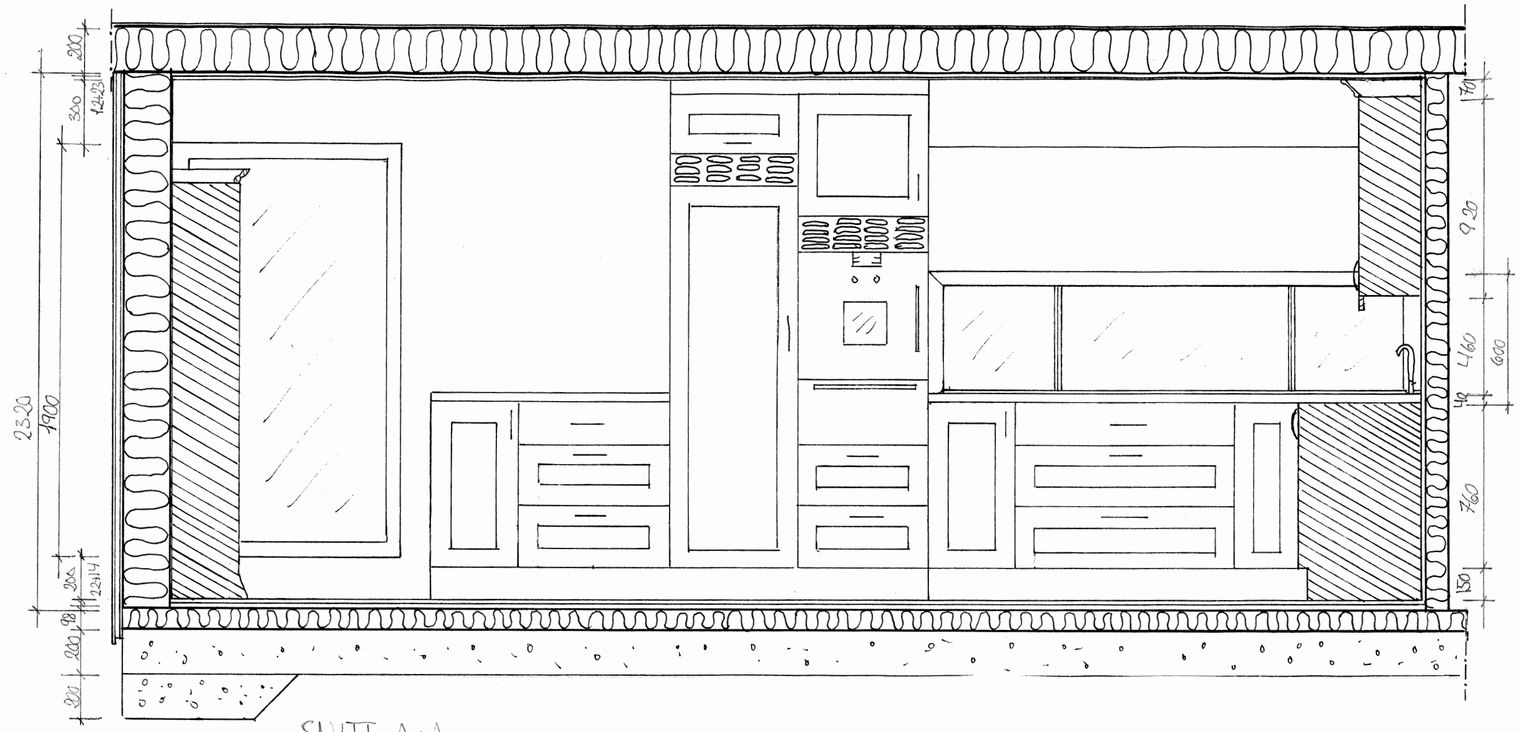

SNITT A:A

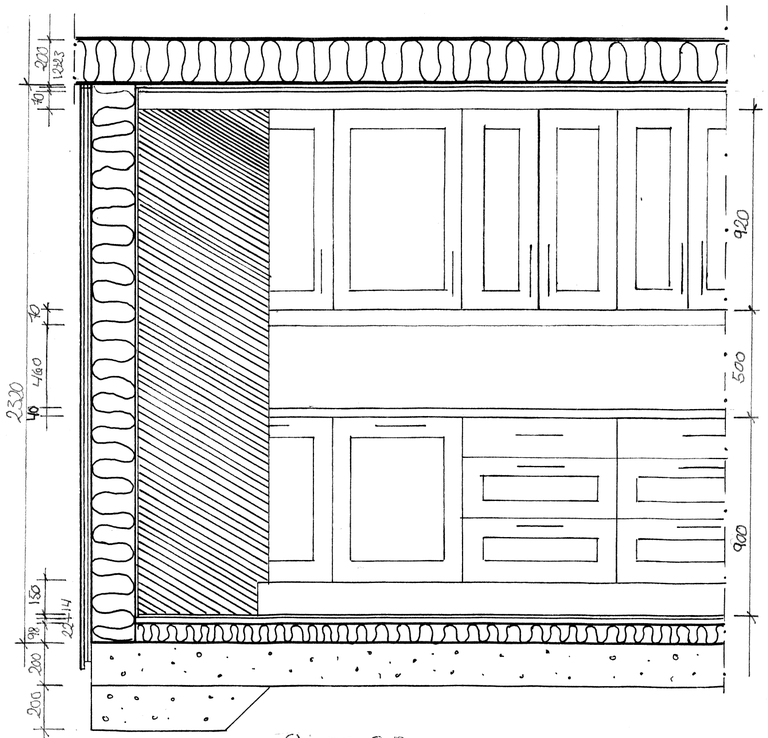

SNITT B:B

SNITT A:A

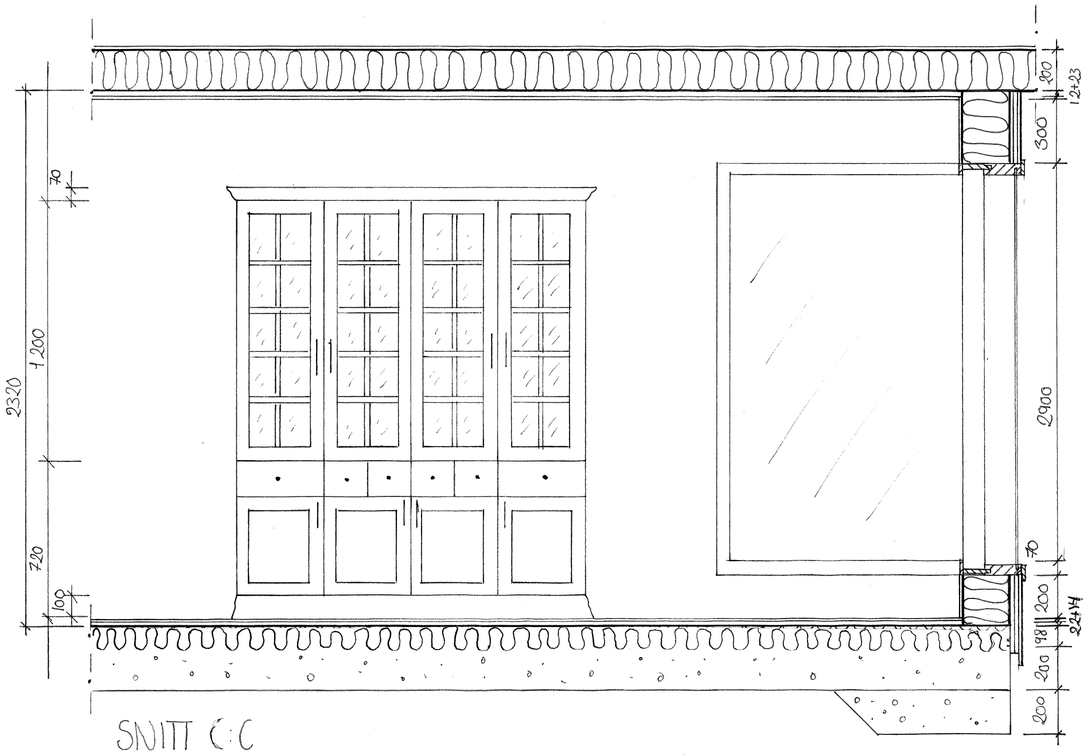

SNITT C:C

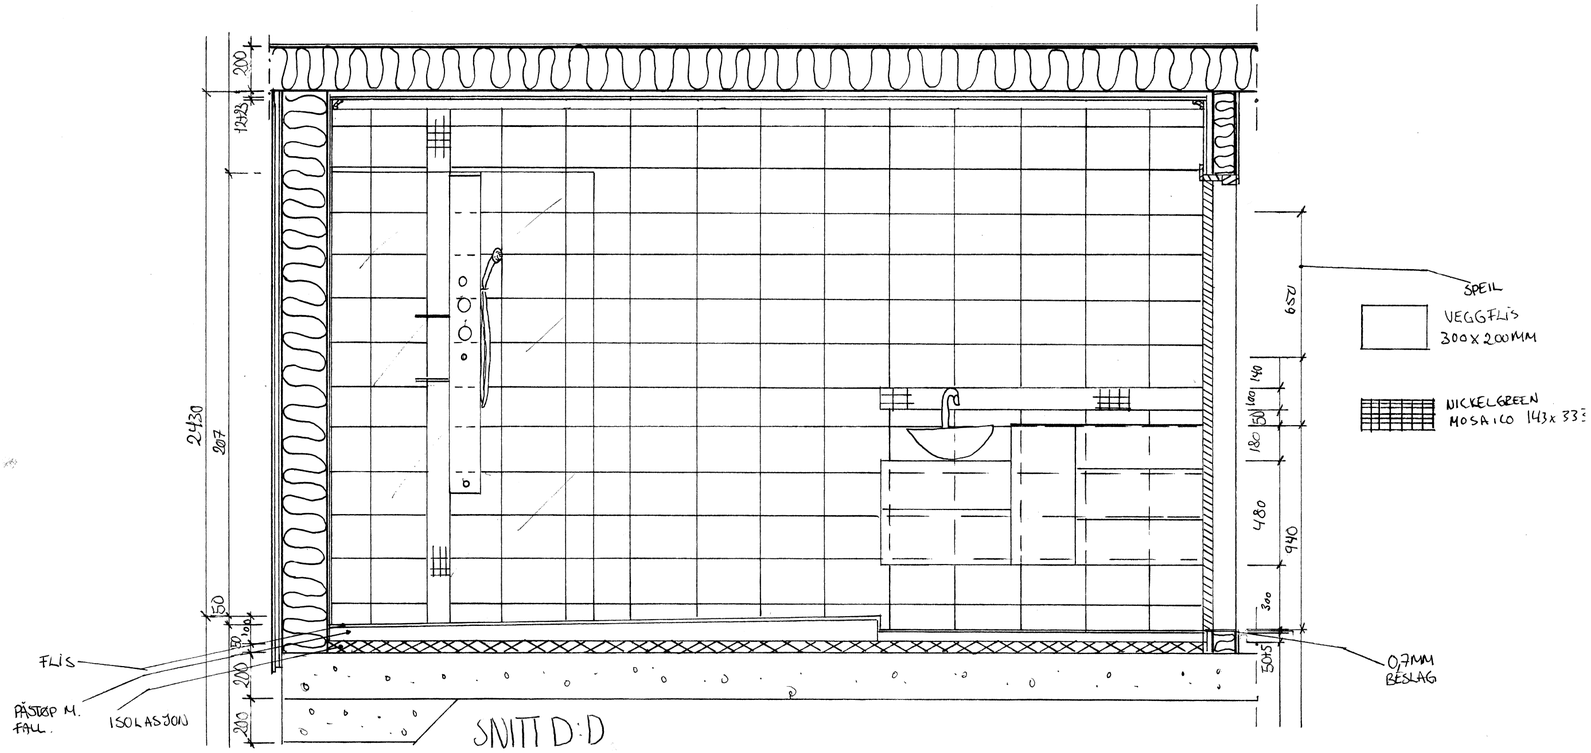
SPEIL
VEGGFLIS
300 X 200 MM
NICKELGREEN
MOSAICO 143 x 33
FLIS
PÅSTØP M.
FALL.
ISOLASJON
0,7MM
BESLAG
SNITT D:D

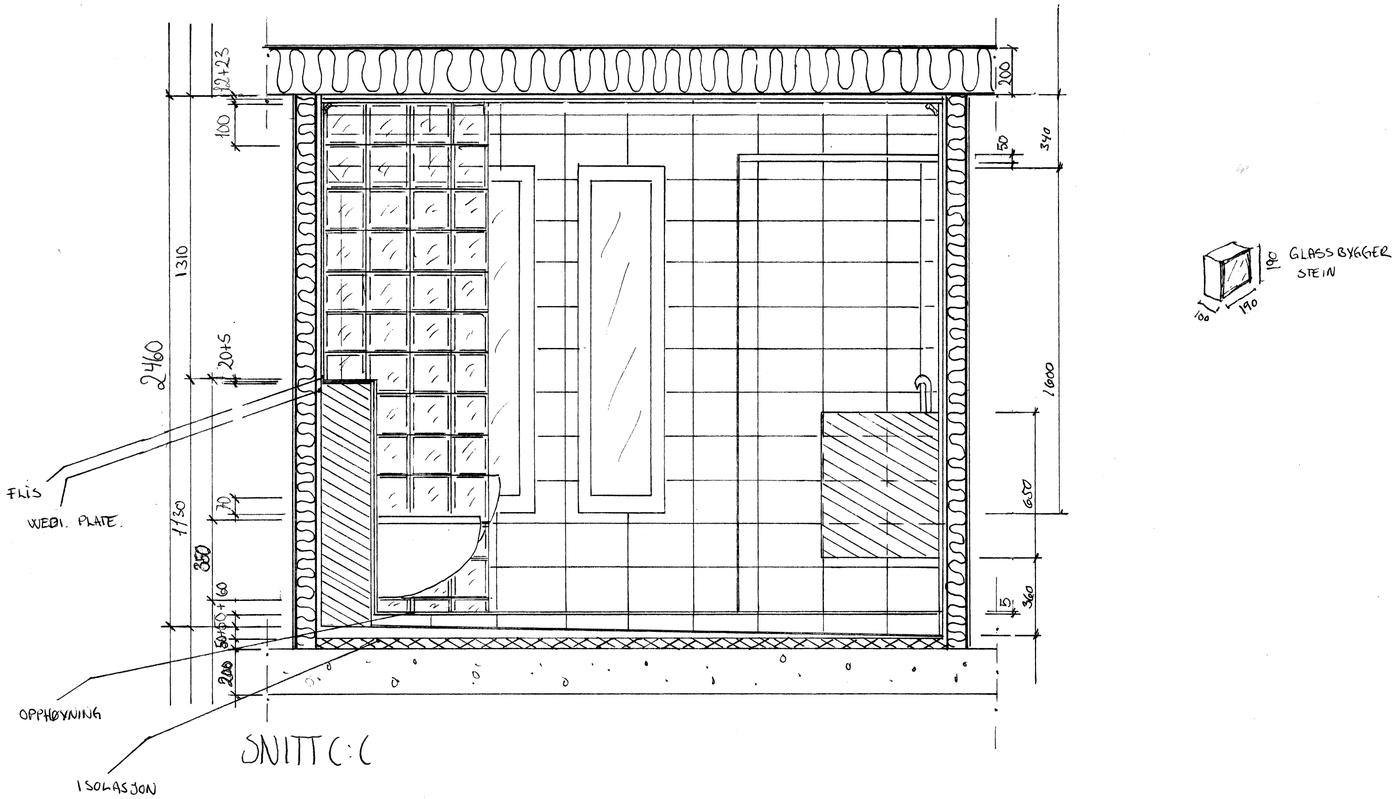
GLASSBYGGER
STEIN
FLIS
WEDI. PLATE.
OPPHØYNING
ISOLASJON
SNITT C:C