

# 1: Moodboard



PROJECT 1 : Surf club  
Dollymount Renovation  
June Therèse M Haugland

BUBBLES!  
16.10.2012  
Studnr: 2831878

2:PLAN 1:50

TERRACE

B

PROJECT 1 : Surf club  
Dollymount Renovation  
June Therèse M Haugland

LEGEND:
EXISTING STRUCTURE
PROPOSAL STRUCTURE
DEMOLISHED STRUCTURE

Ceramic tiles

Floor tiles  
Rovere Grip,  
mate finish  
Hoganas


A

Main entrance  
Sliding doors

10450

CHANGING  
ROOM WOMEN

RECEPTION

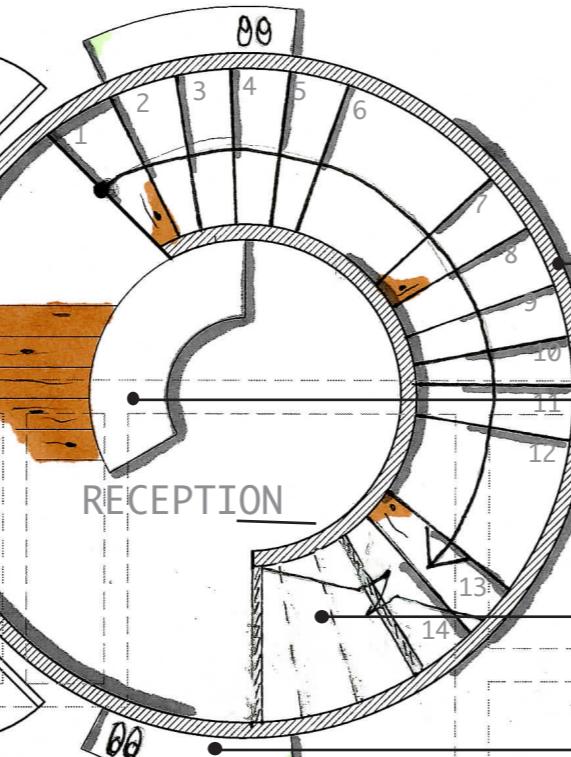

SURF  
BOARD  
STORAGE

CHANGING  
ROOM MEN

10450

B

TERRACE

A

Glaswall  
with water and air.  
Purple led lighting.

Reception desk Front:  
3Form seaweed glass +  
white out  
Topp: Formica Limides  
Strand

Staff lockers

Shoes shelves

3Form seaweed  
glass + white out

Bench  
Lockers




BUBBLES!

16.10.2012  
Studnr: 2831878

GROUND FLOOR PLAN 1:50


3:PLAN 1:50

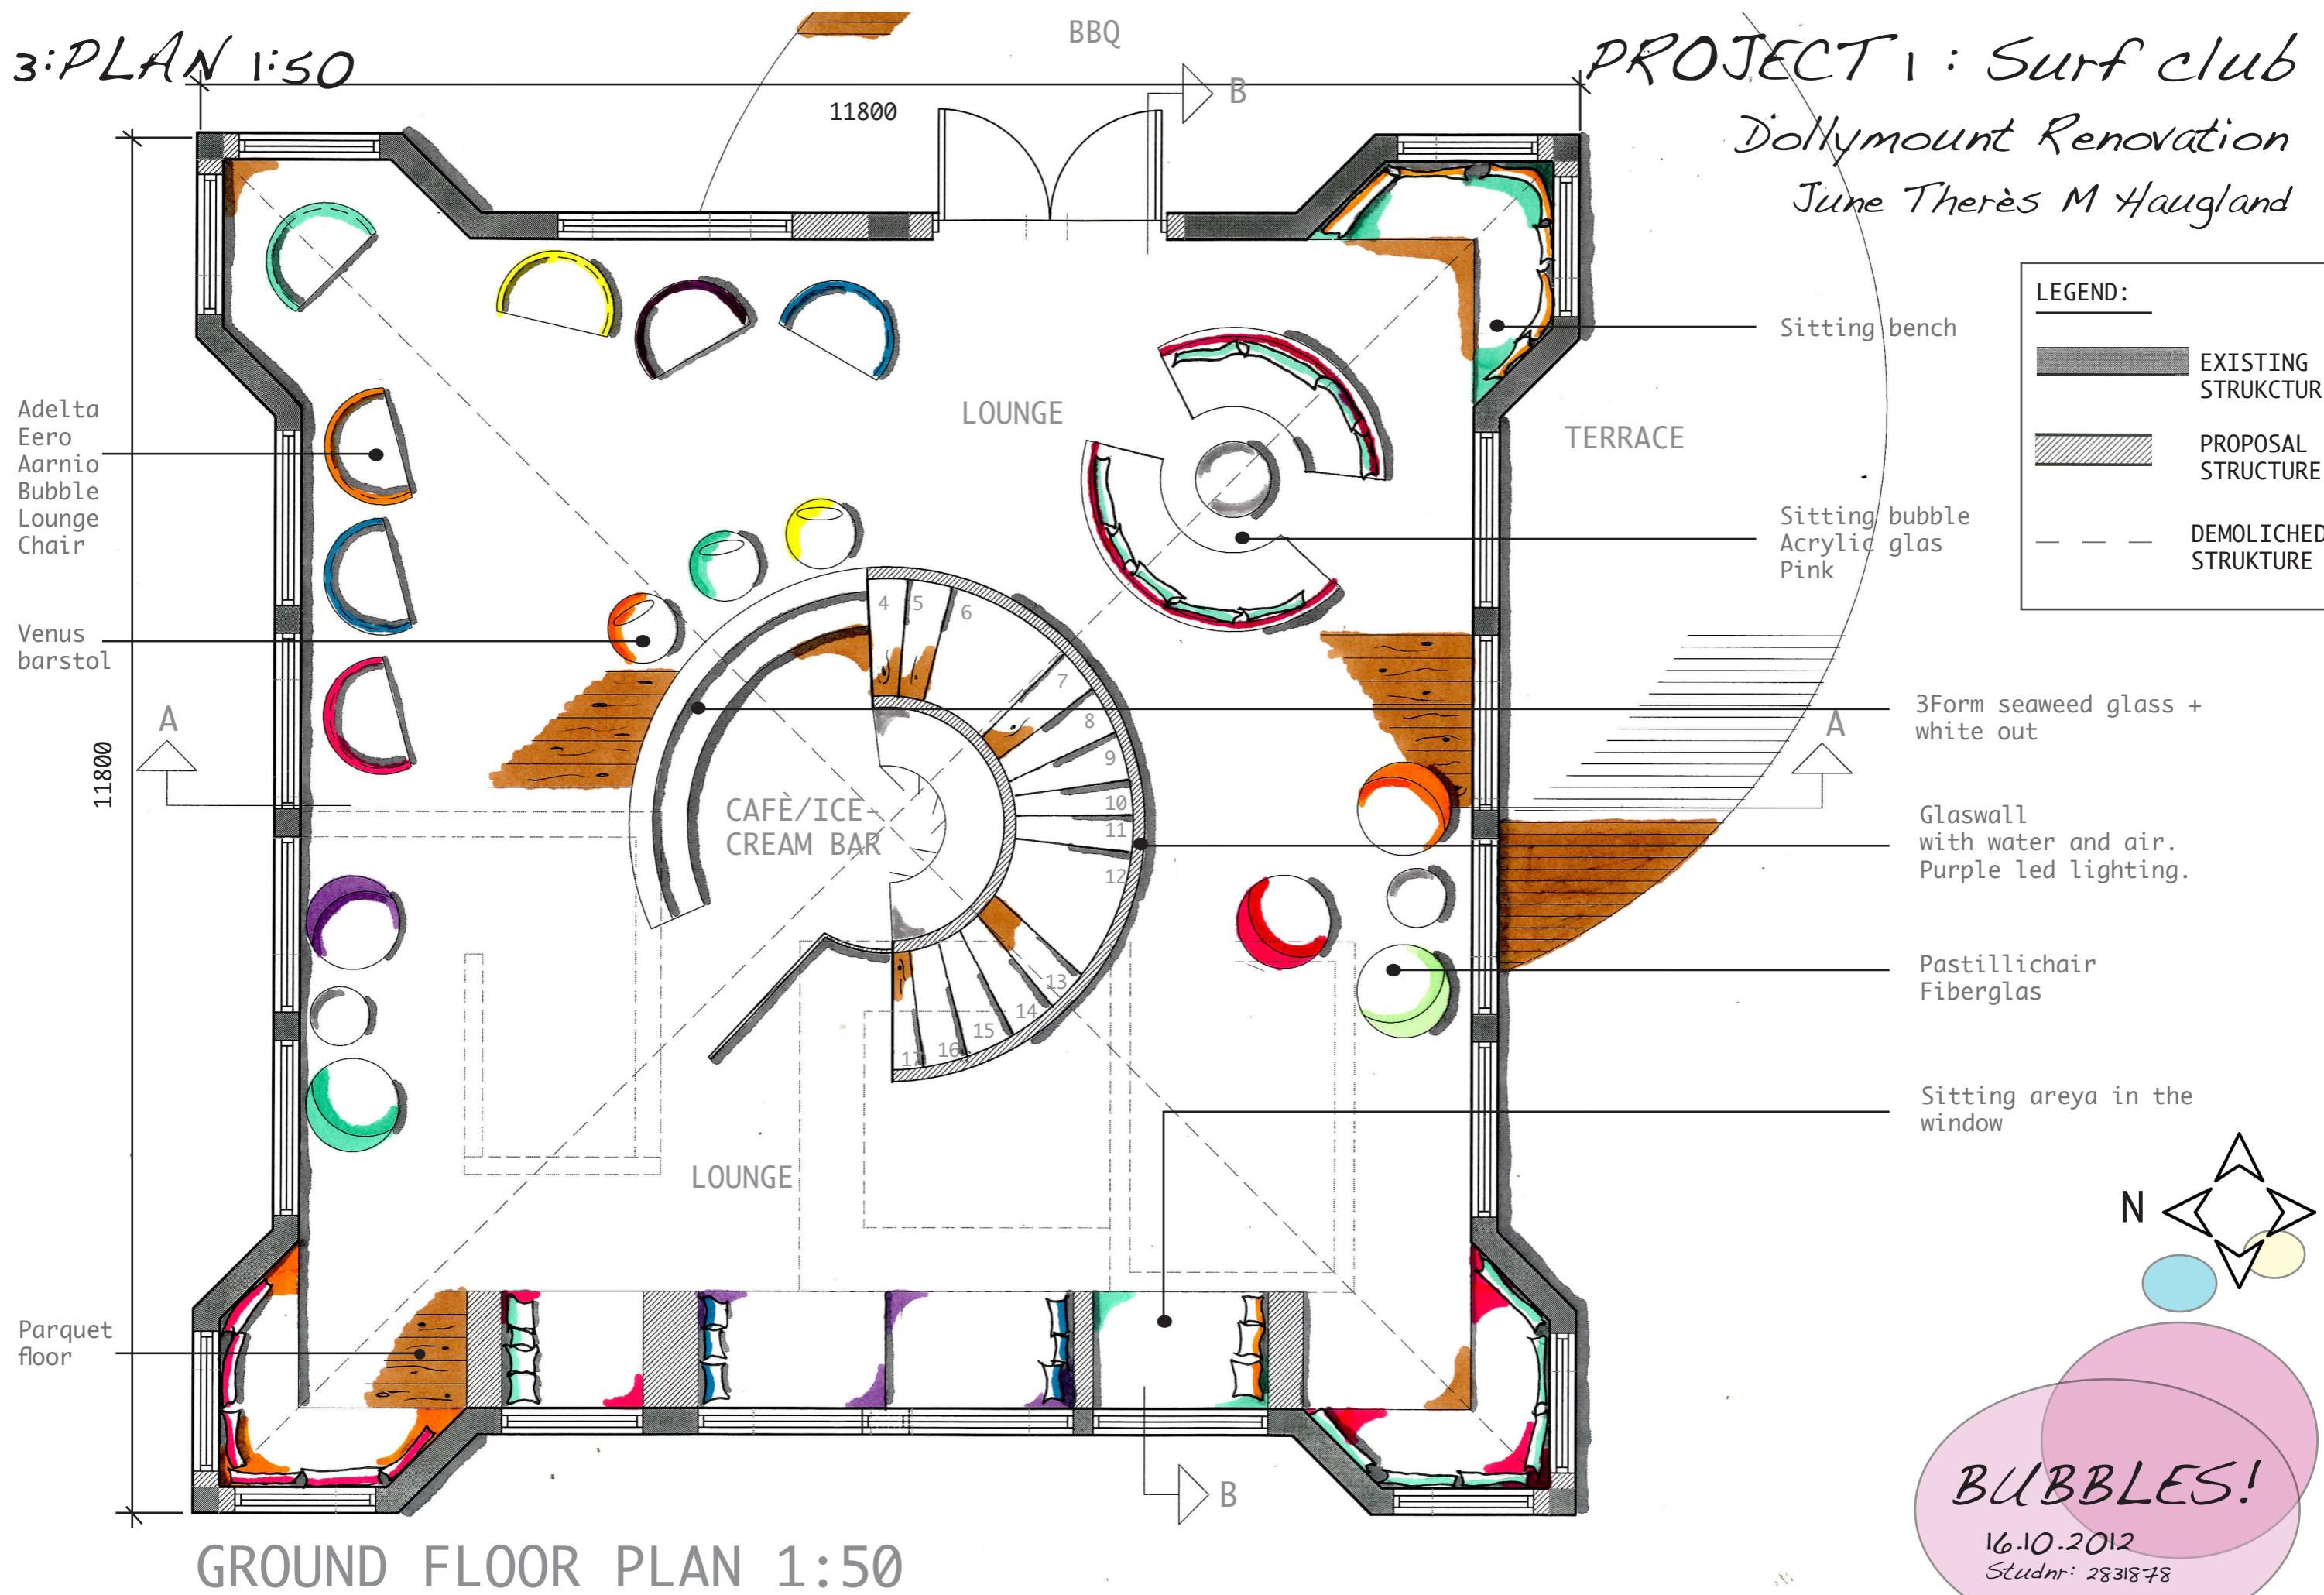


4: Elevation 1:50

PROJECT 1 : Surf club  
Dollymount Renovation  
June Therèse M Haugland


ROOF LEVEL  
RL 3129

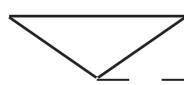


CEILING LEVEL  
CL 2922

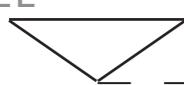



FIRST FLOOR  
FF2870

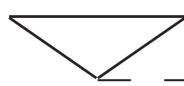

GROUND FLOOR  
GF 170

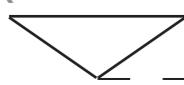

GROUND LEVEL  
GL 0

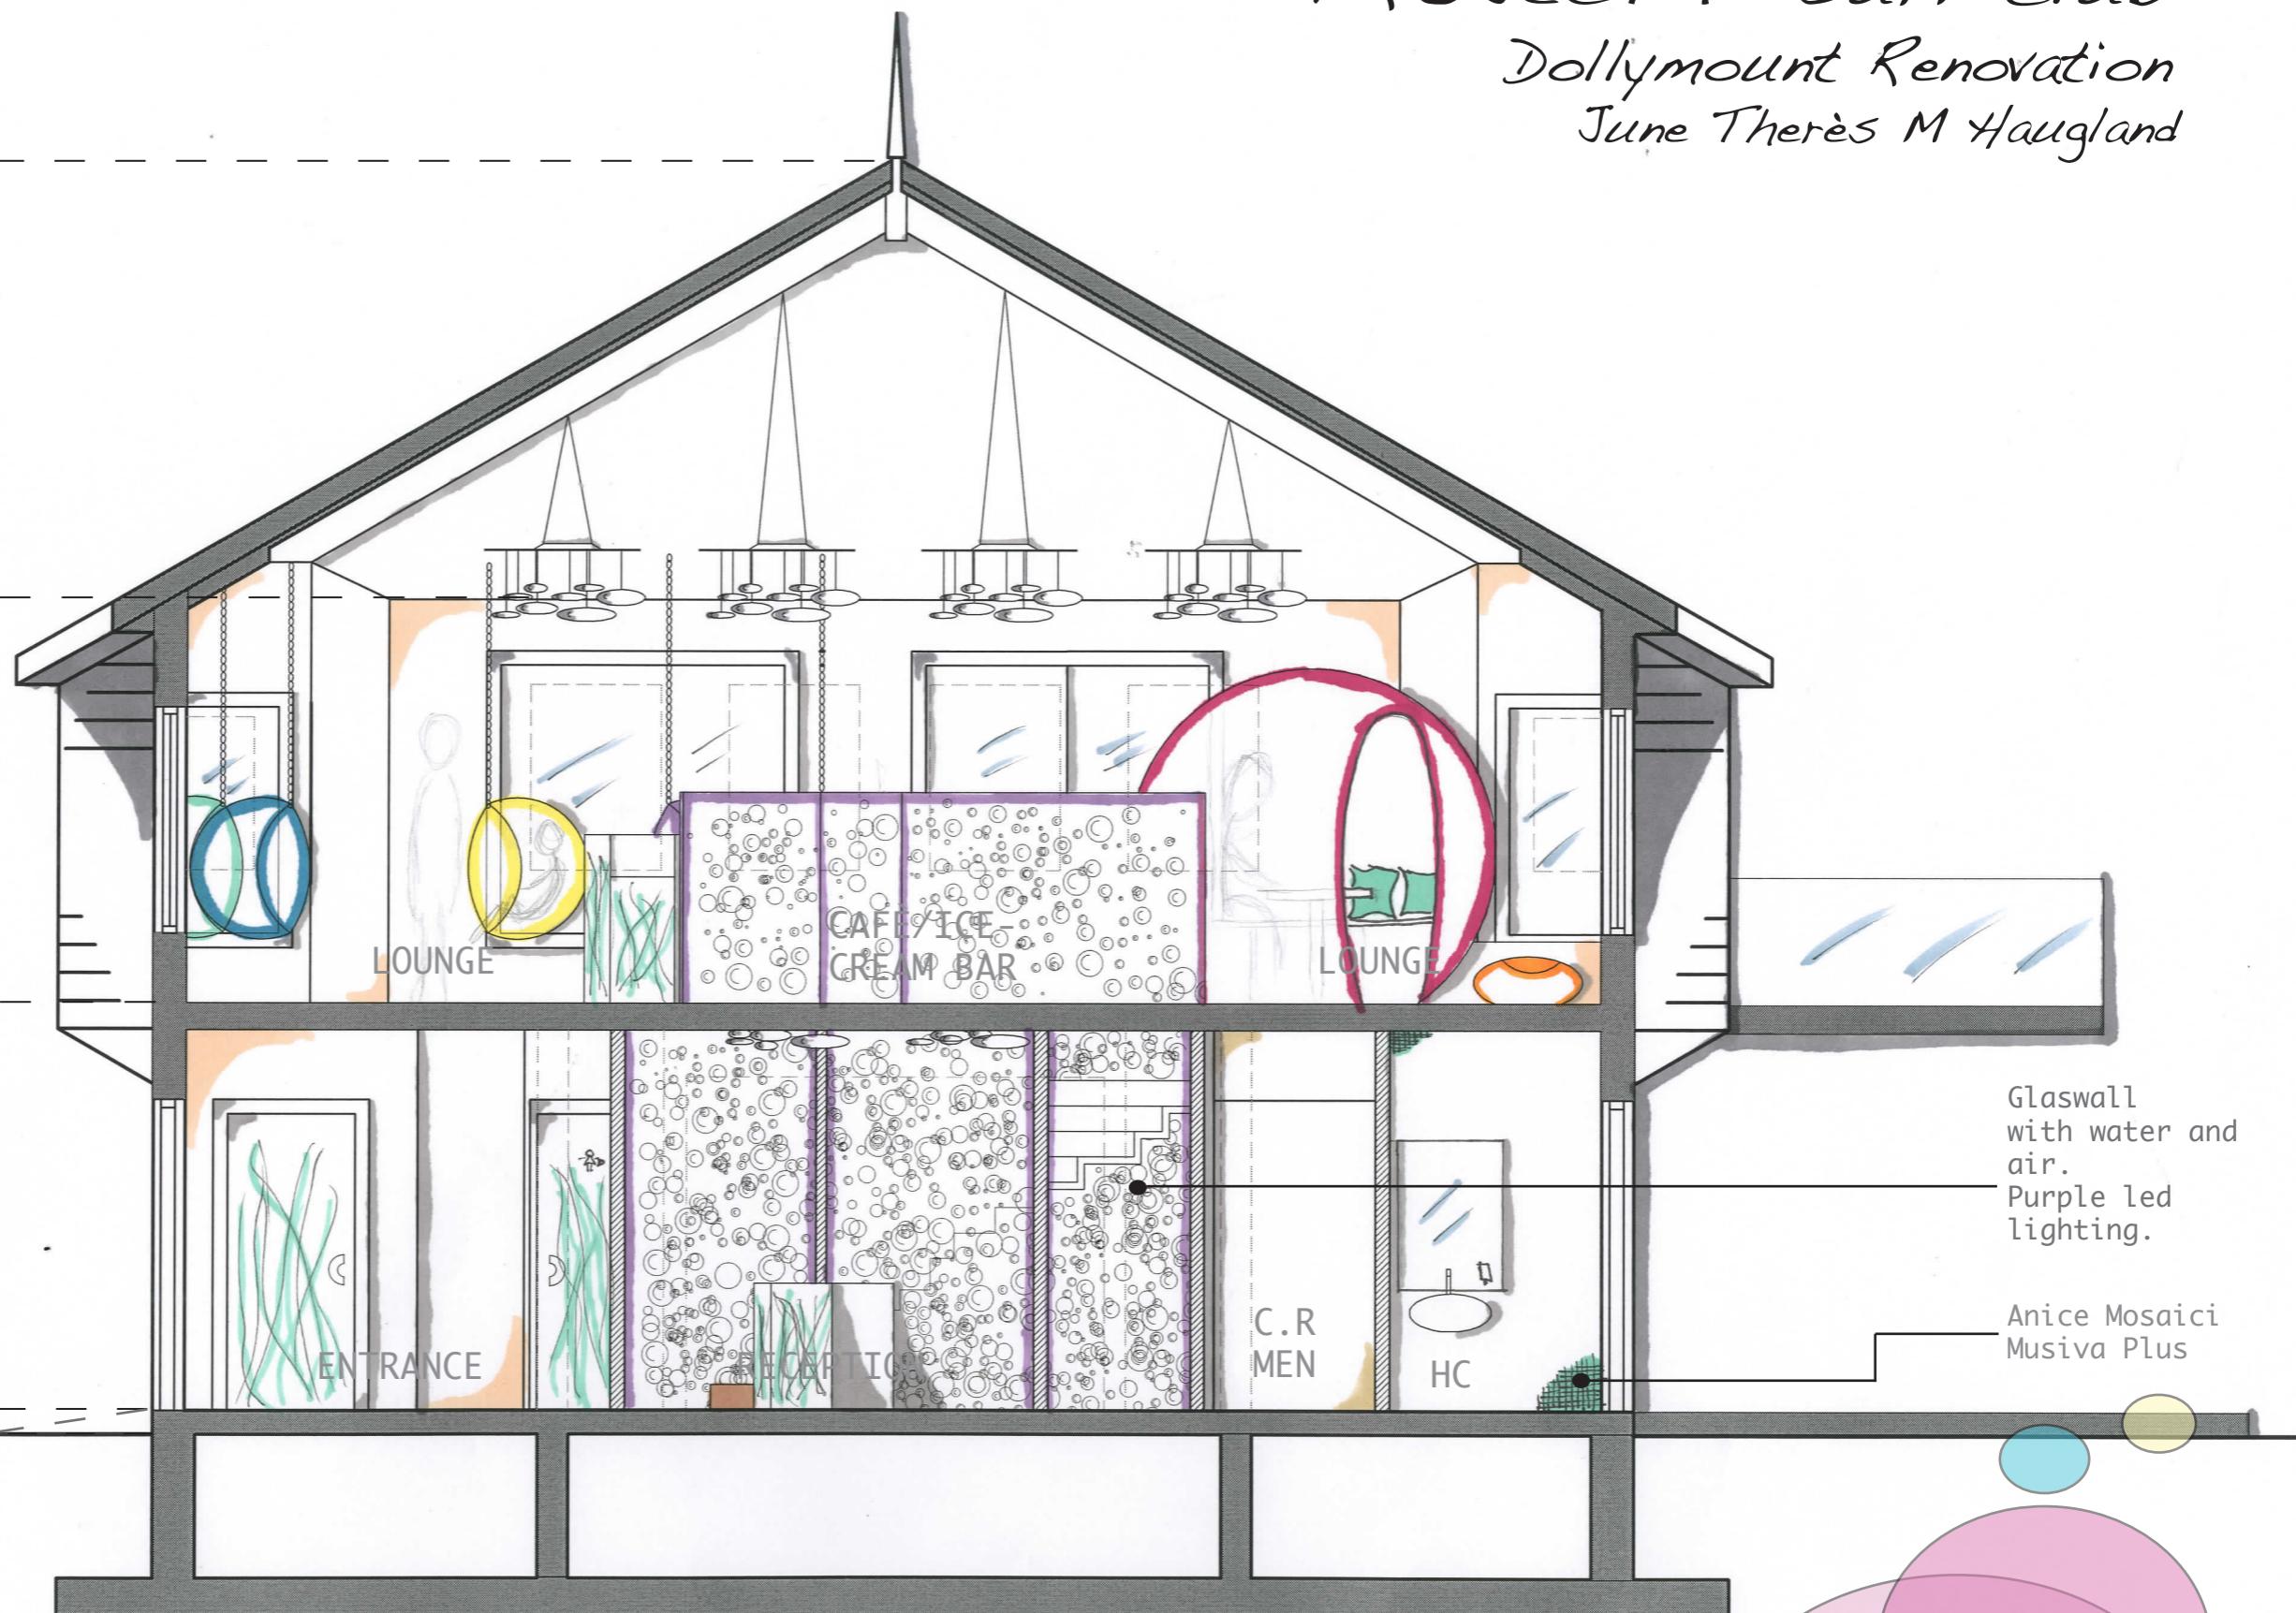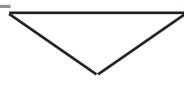

ELEVATION B:B 1:50

5:Elevation 1:50

ROOF LEVEL  
RL 3129

PROJECT 1 : Surf club


Dollymount Renovation  
June Therèse M Haugland

CEILING LEVEL  
CL 2922

FIRST FLOOR  
FF2870

GROUND FLOOR  
GF 170

GROUND LEVEL  
GL 0

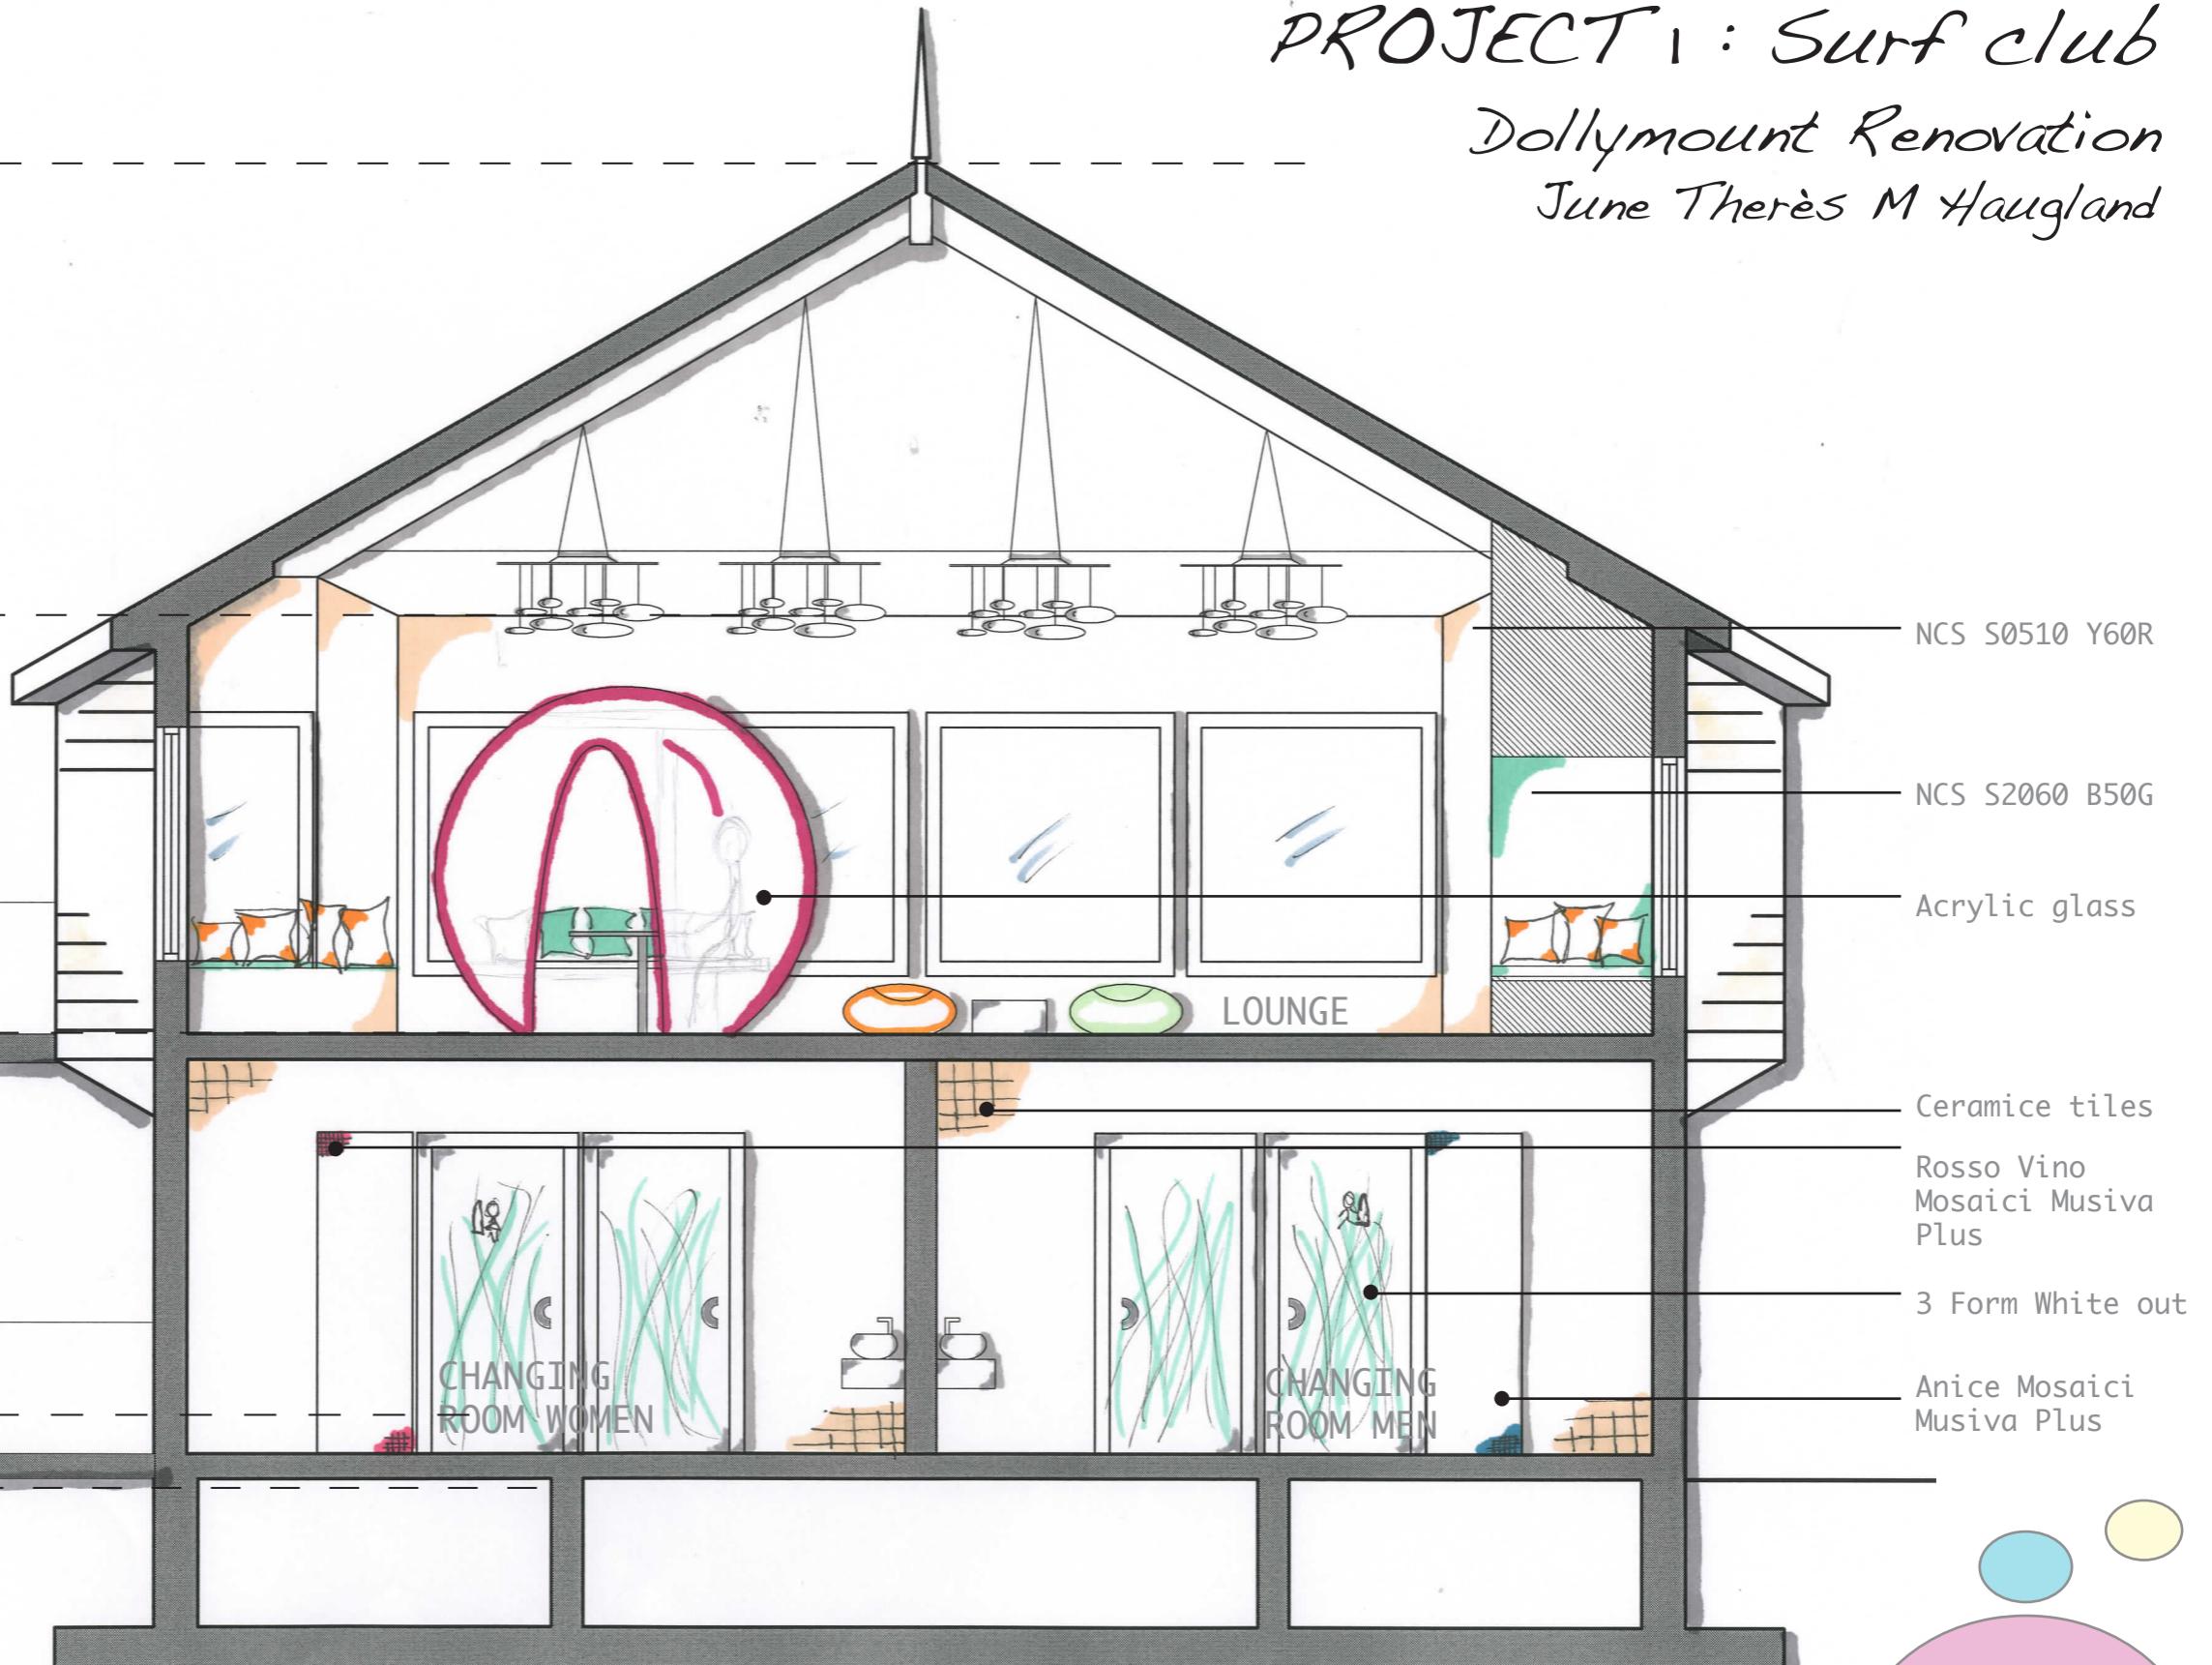

ELEVATION A:A 1:50

BUBBLES!

16.10.2012  
Studnr: 2831878

6:Section 1:50


PROJECT 1 : Surf club  
Dollymount Renovation  
June Therèse M Haugland



BUBBLES!  
16.10.2012  
Studnr: 2831878

7: Elevation 1:50

PROJECT 1 : Surf club  
Dollymount Renovation  
June Therèse M Haugland

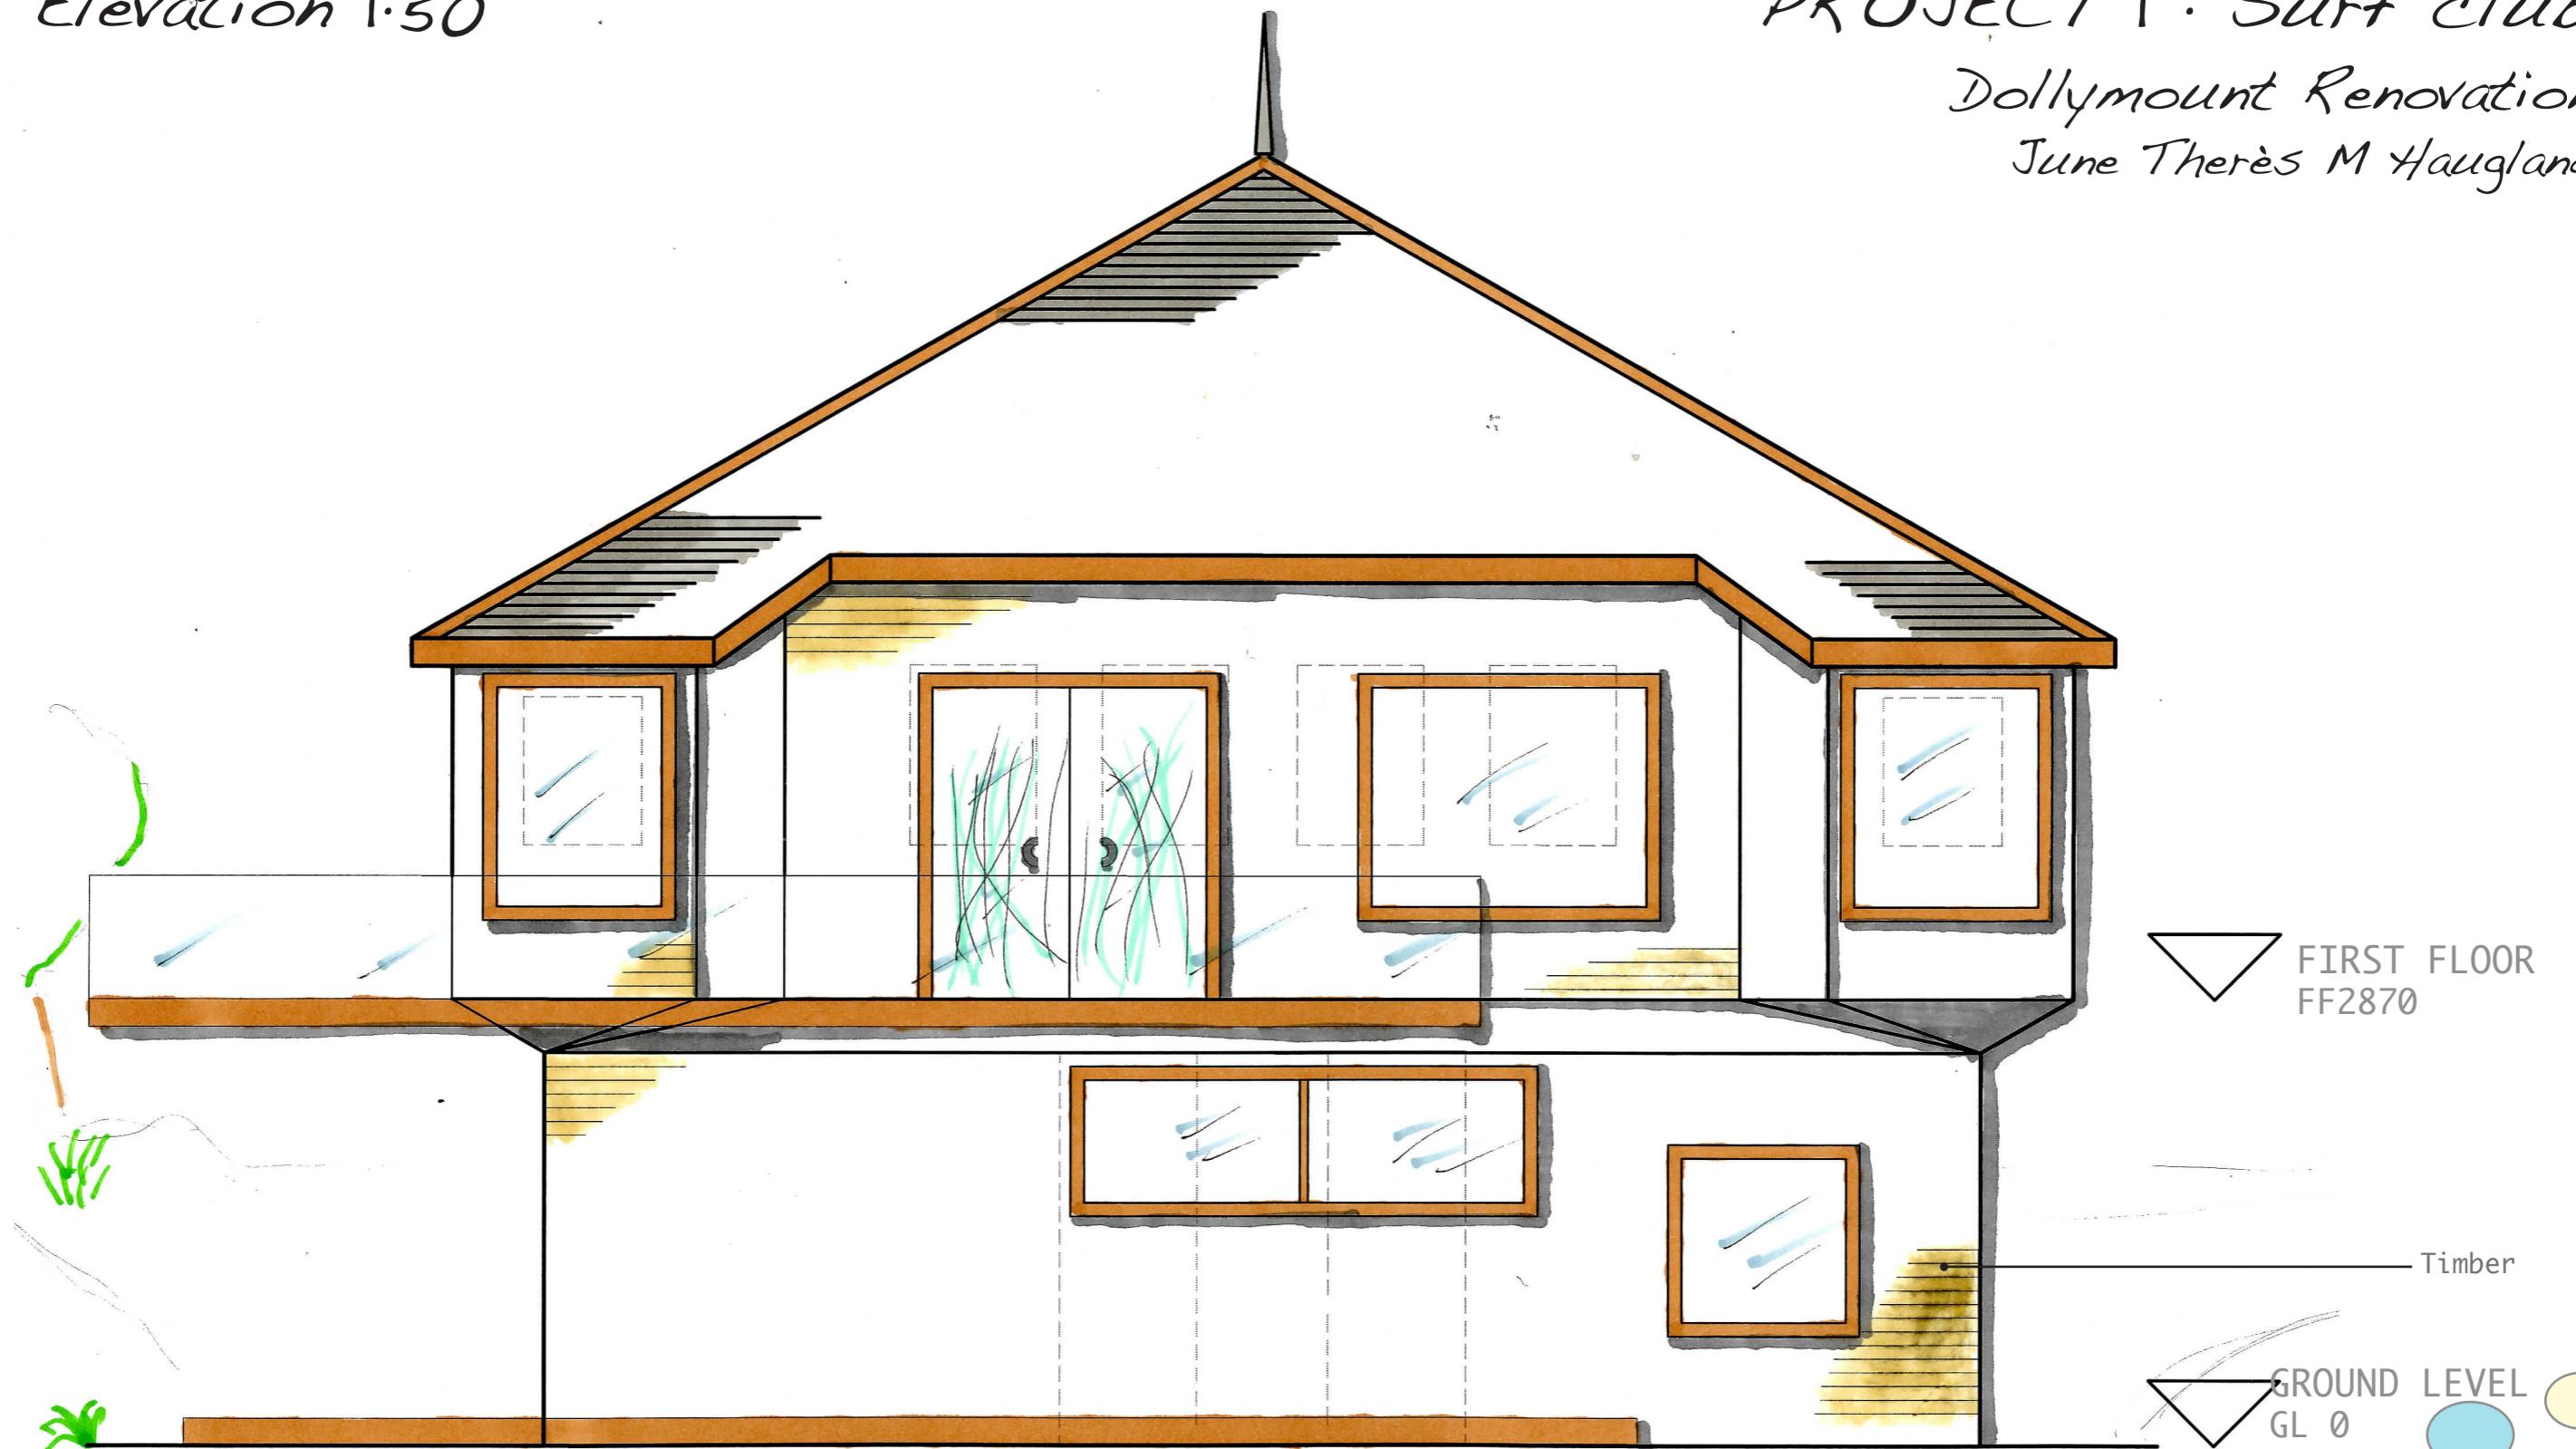


SECTION EAST 1:50

BUBBLES!

16.10.2012  
Studnr: 2831878

8:Elevation 1:50

PROJECT 1 : Surf club  
Dollymount Renovation  
June Thérèse M Haugland

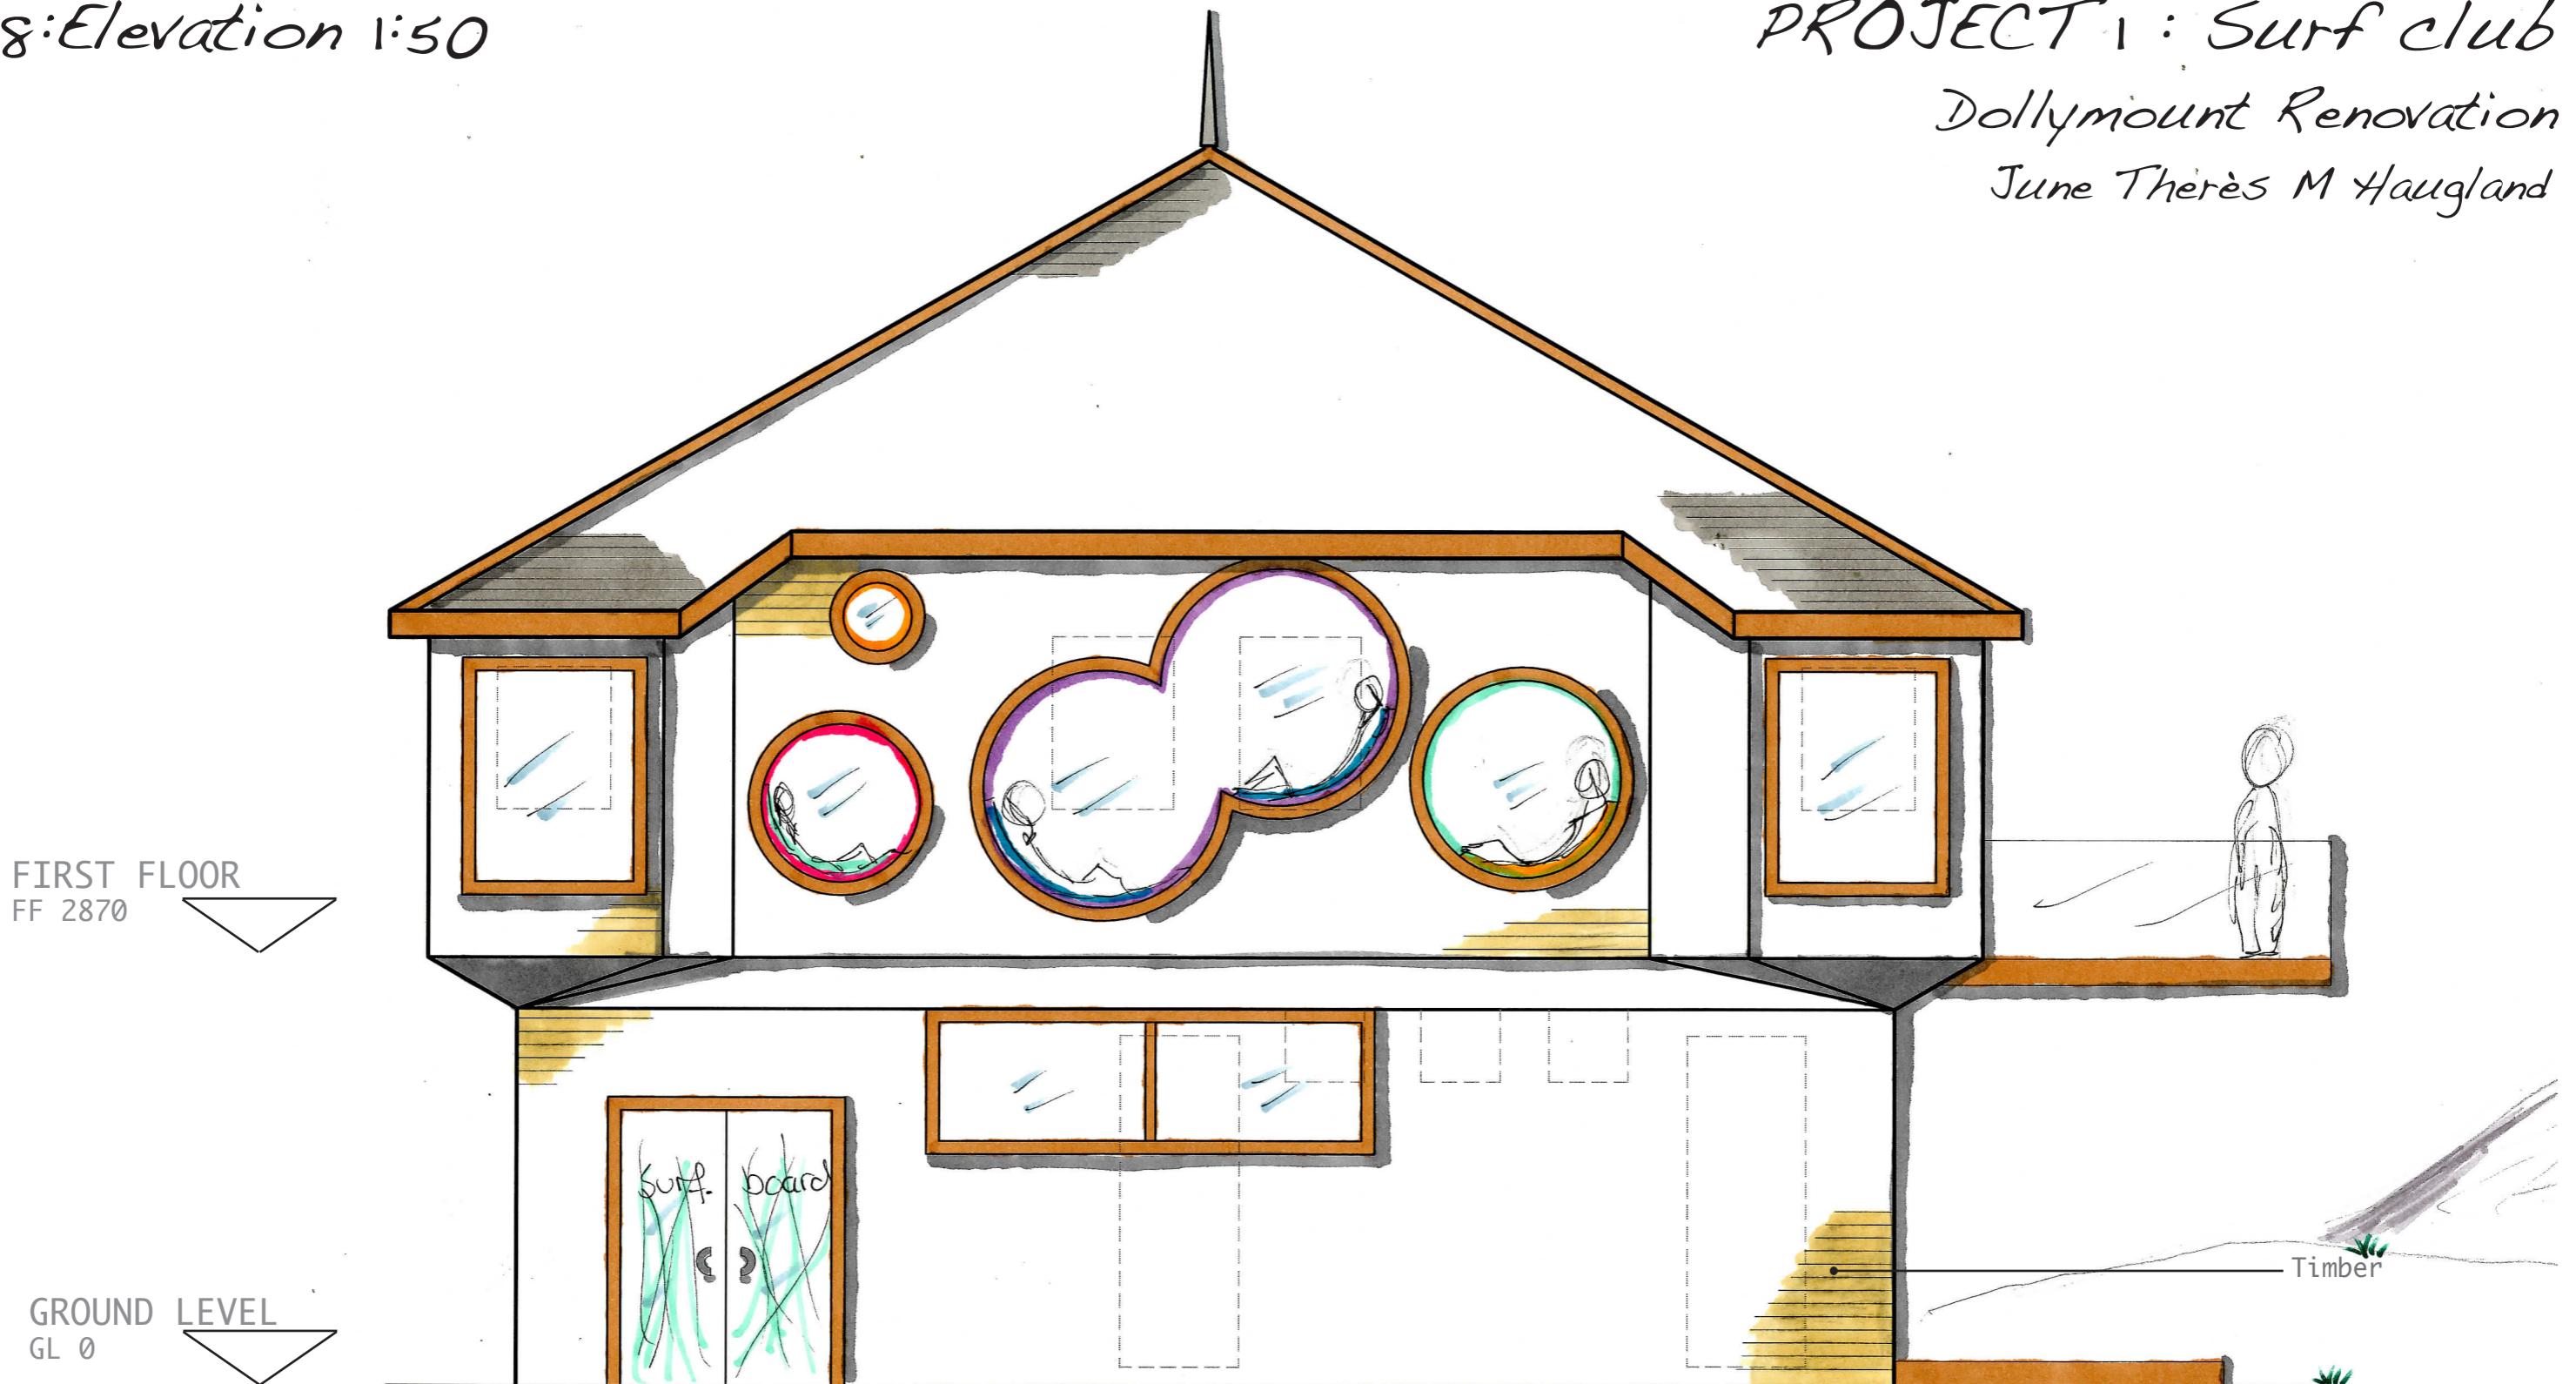


SECTION WEST 1:50



9:Elevation 1:50

PROJECT 1 : Surf club  
Dollymount Renovation  
June Therèse M Haugland

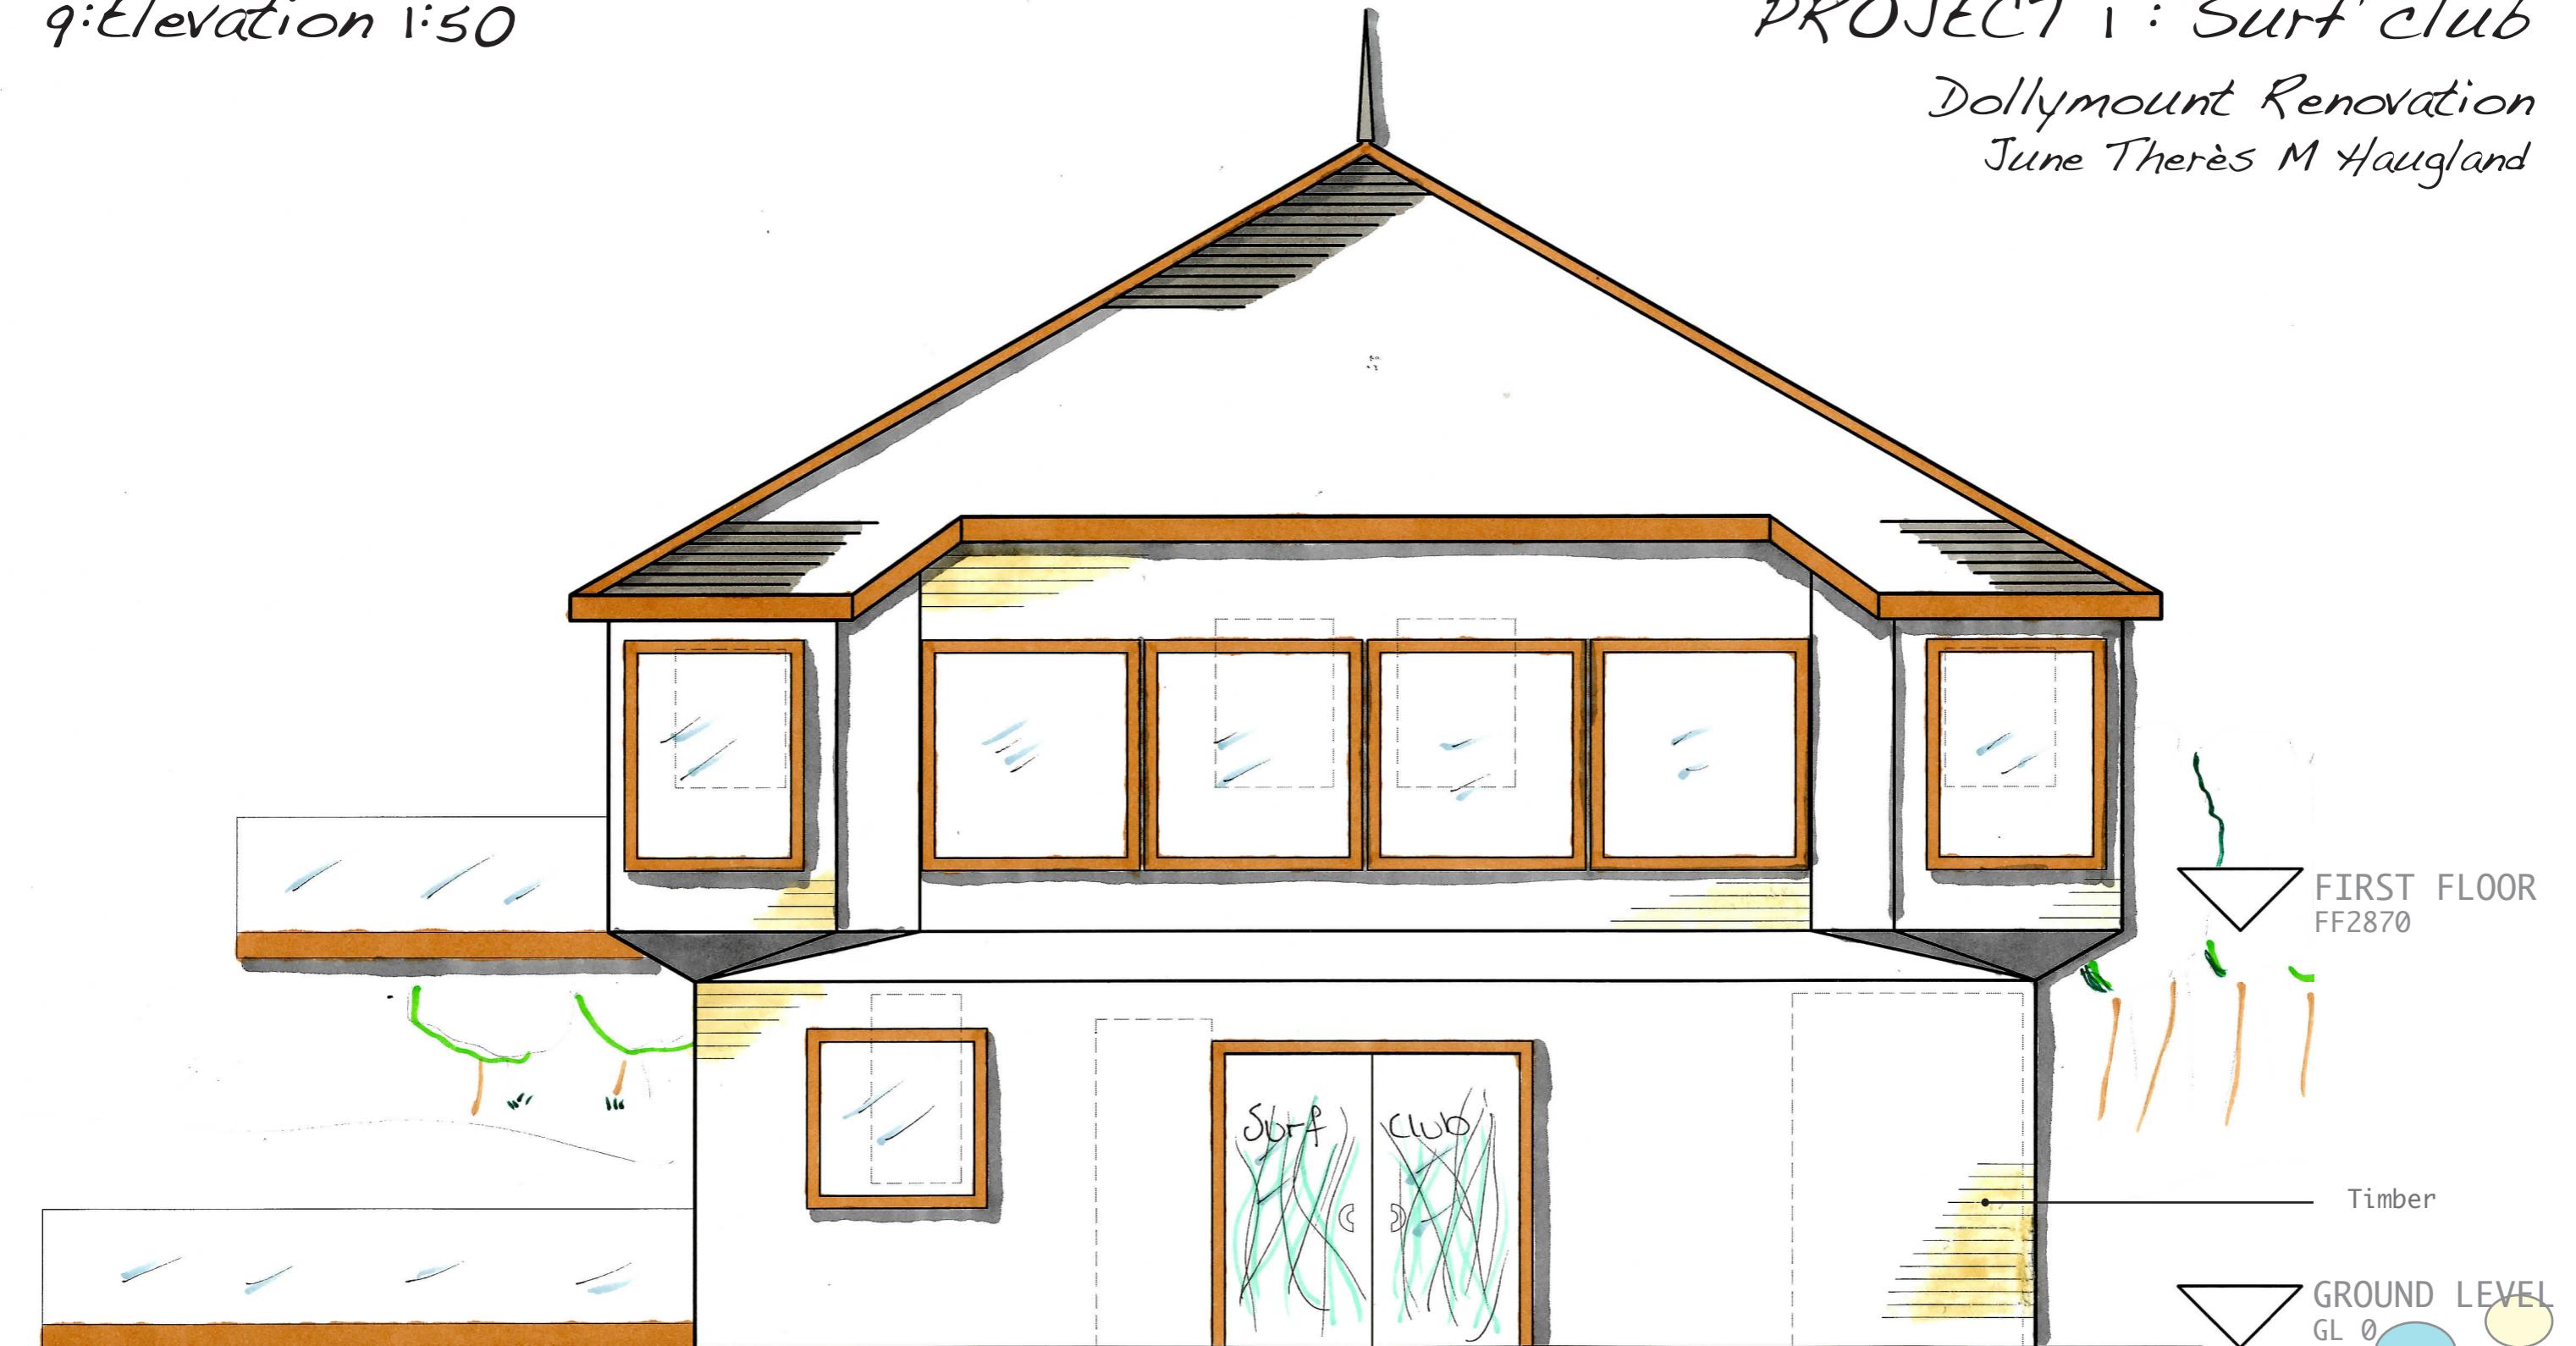

SECTION NORTH 1:50

BUBBLES!

16.10.2012  
Studnr: 2831878

# 10: Reception



PROJECT 1 : Surf club  
Dollymount Renovation  
June Therèse M Haugland

Skydro soffitto  
Led Artemide



Glaswall  
with water and  
air.  
Purple led  
lighting.




3Form seaweed glass  
+ white out

Floor tiles Rovere  
matte



II: Outside


PROJECT 1 : Surf club  
Dollymount Renovation  
June Therèse M Haugland

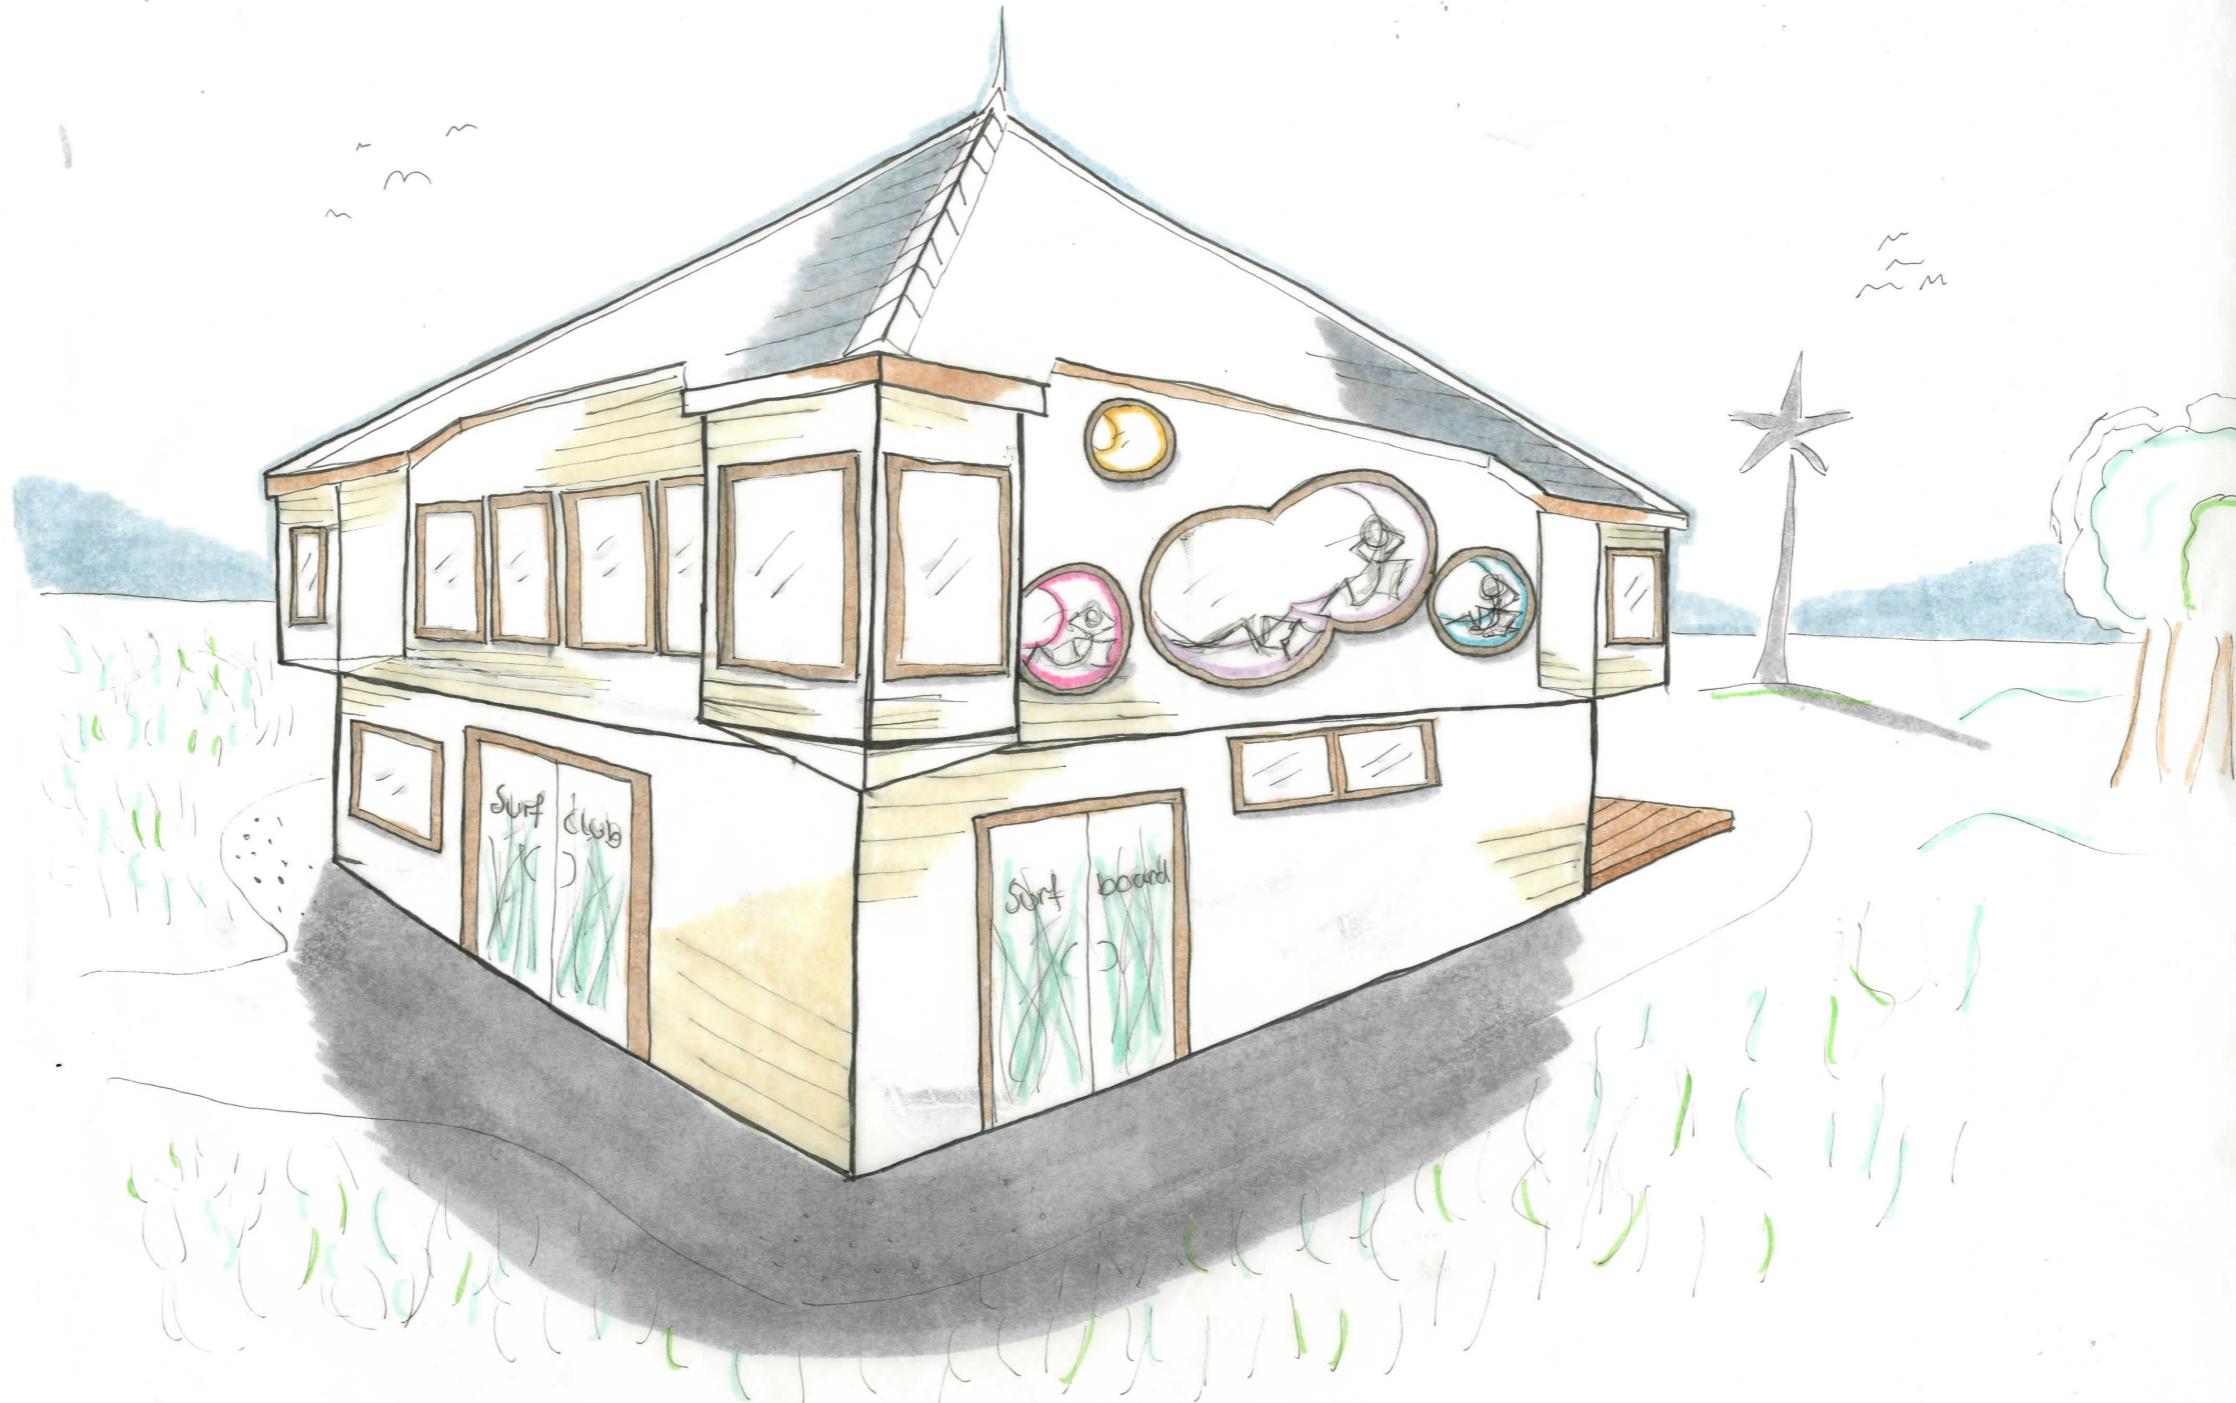

# 12:CafÈ/Ice Cream bar


# PROJECT 1 : Surf club

Dollymount Renovation  
June Therèse M Haugland

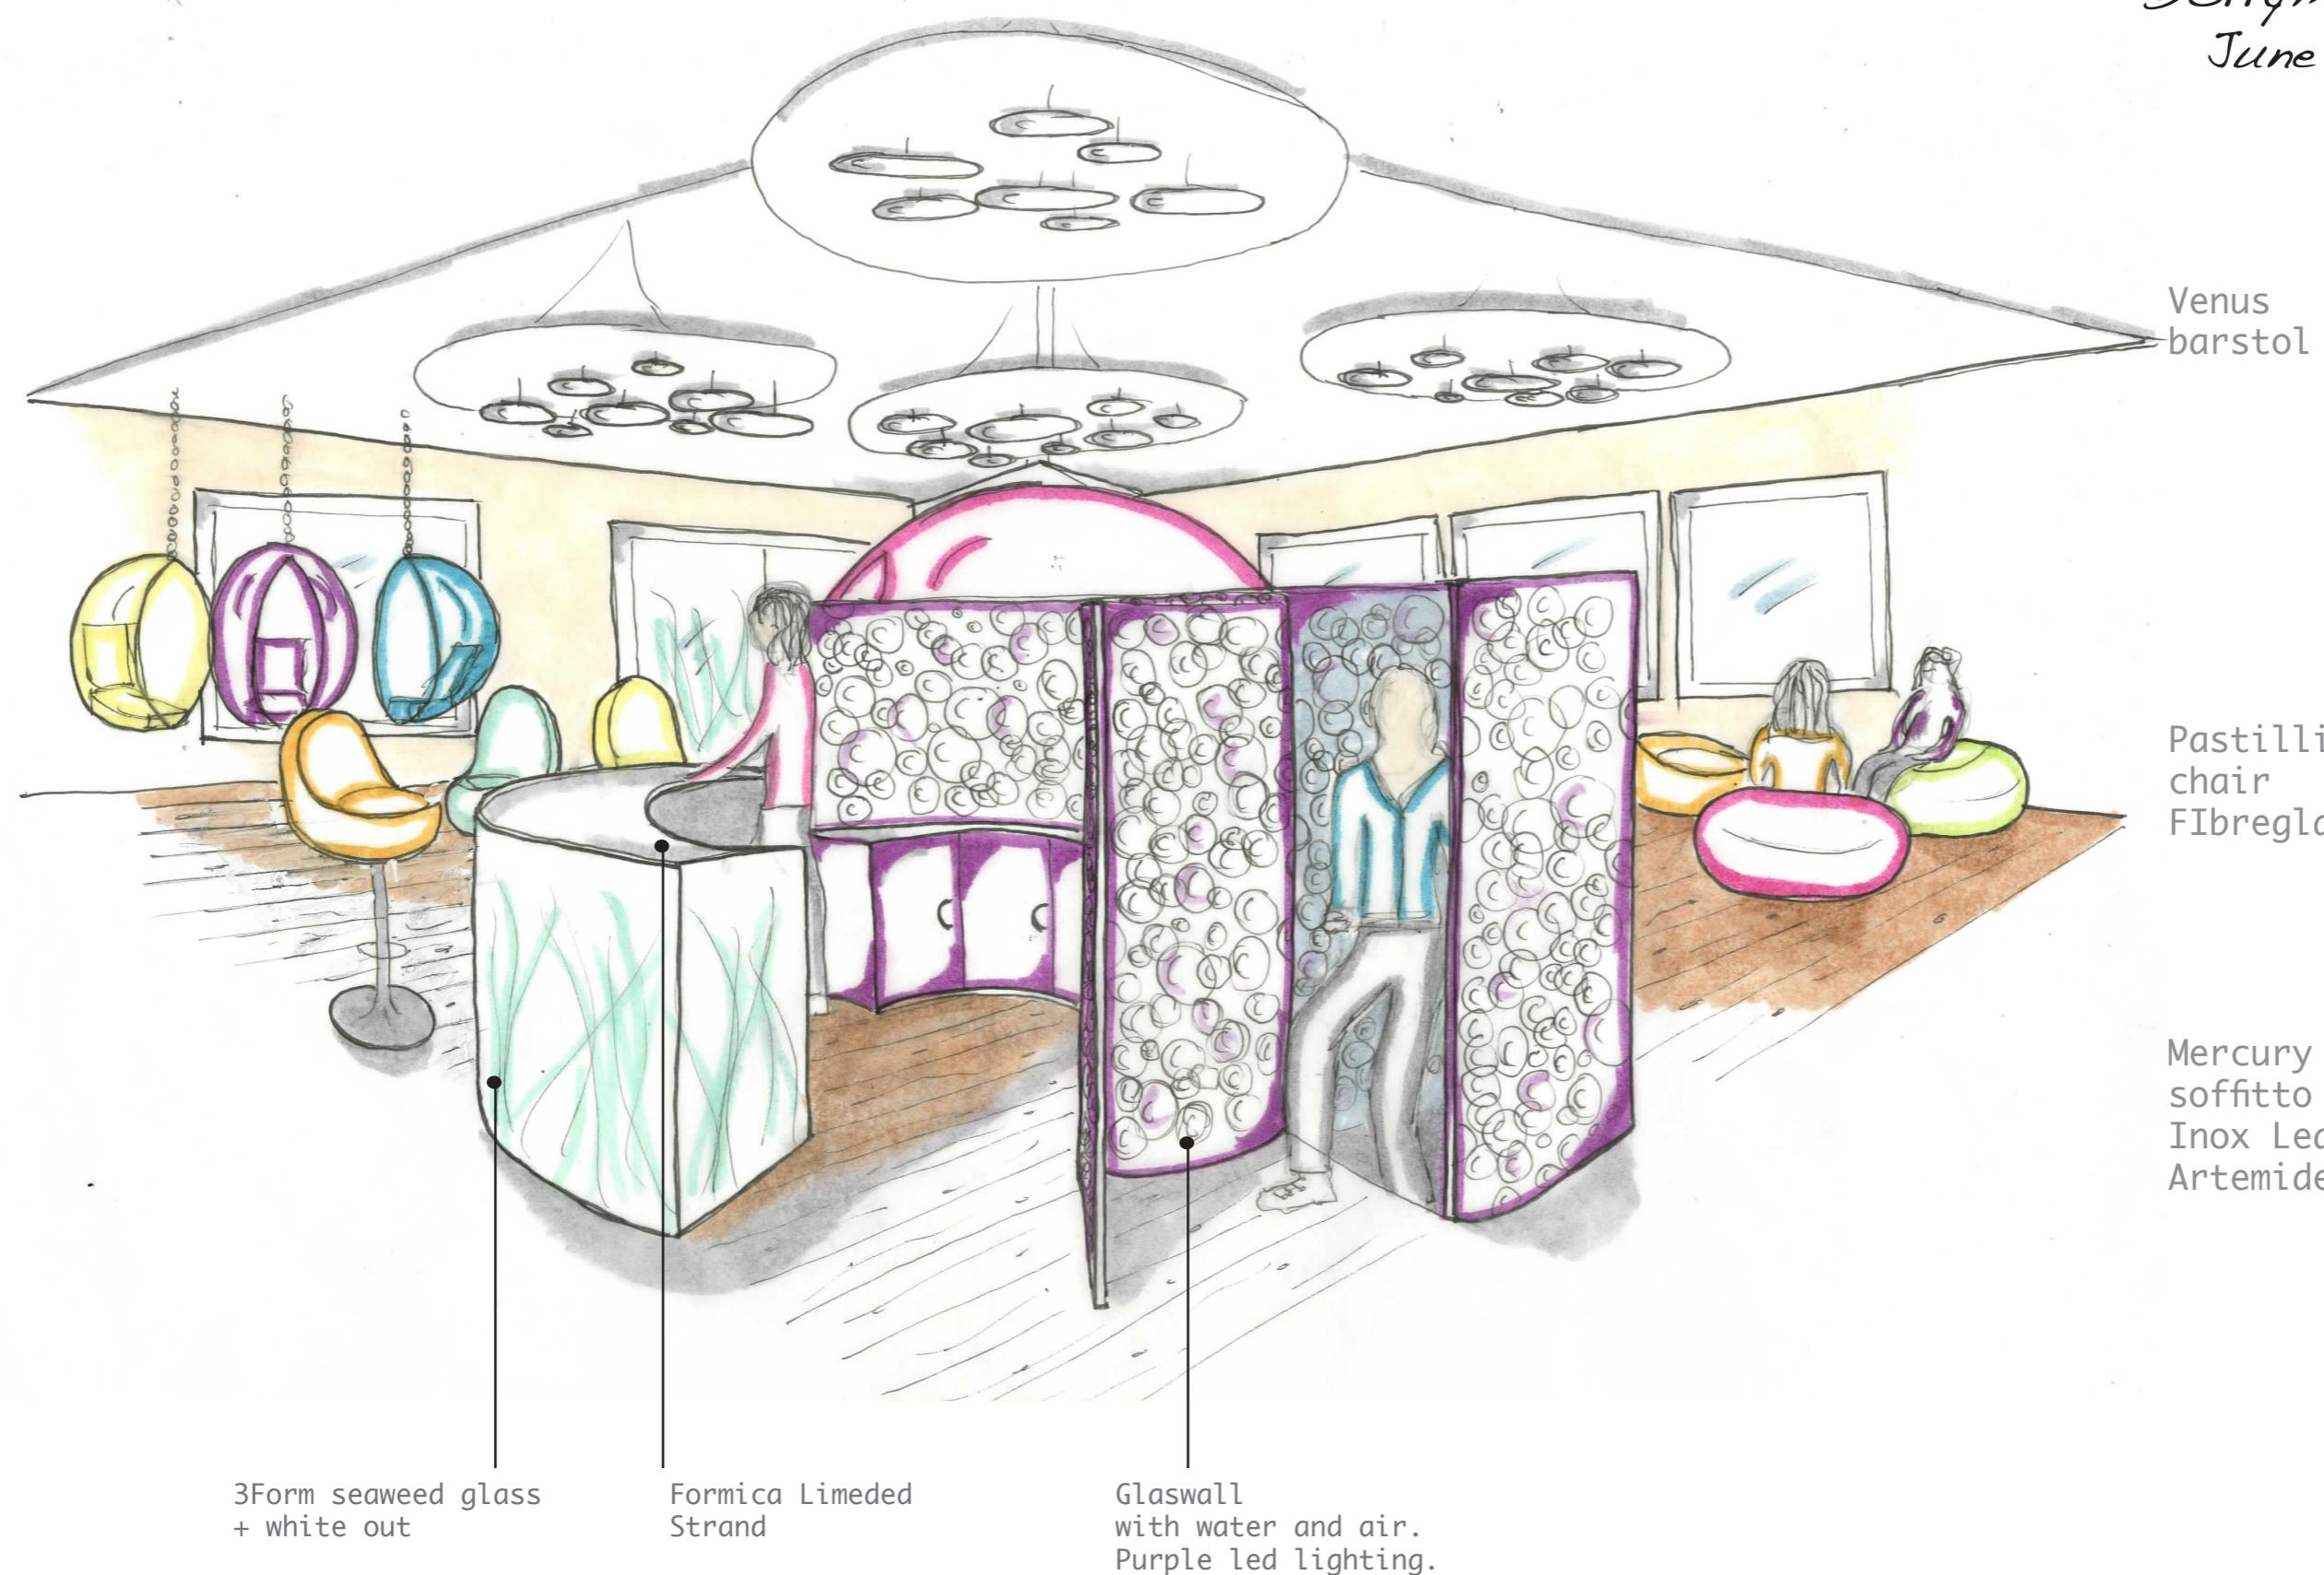

13:Lounge with bubble chairs

PROJECT 1 : Surf club  
Dollymount Renovation  
June Therèse M Haugland

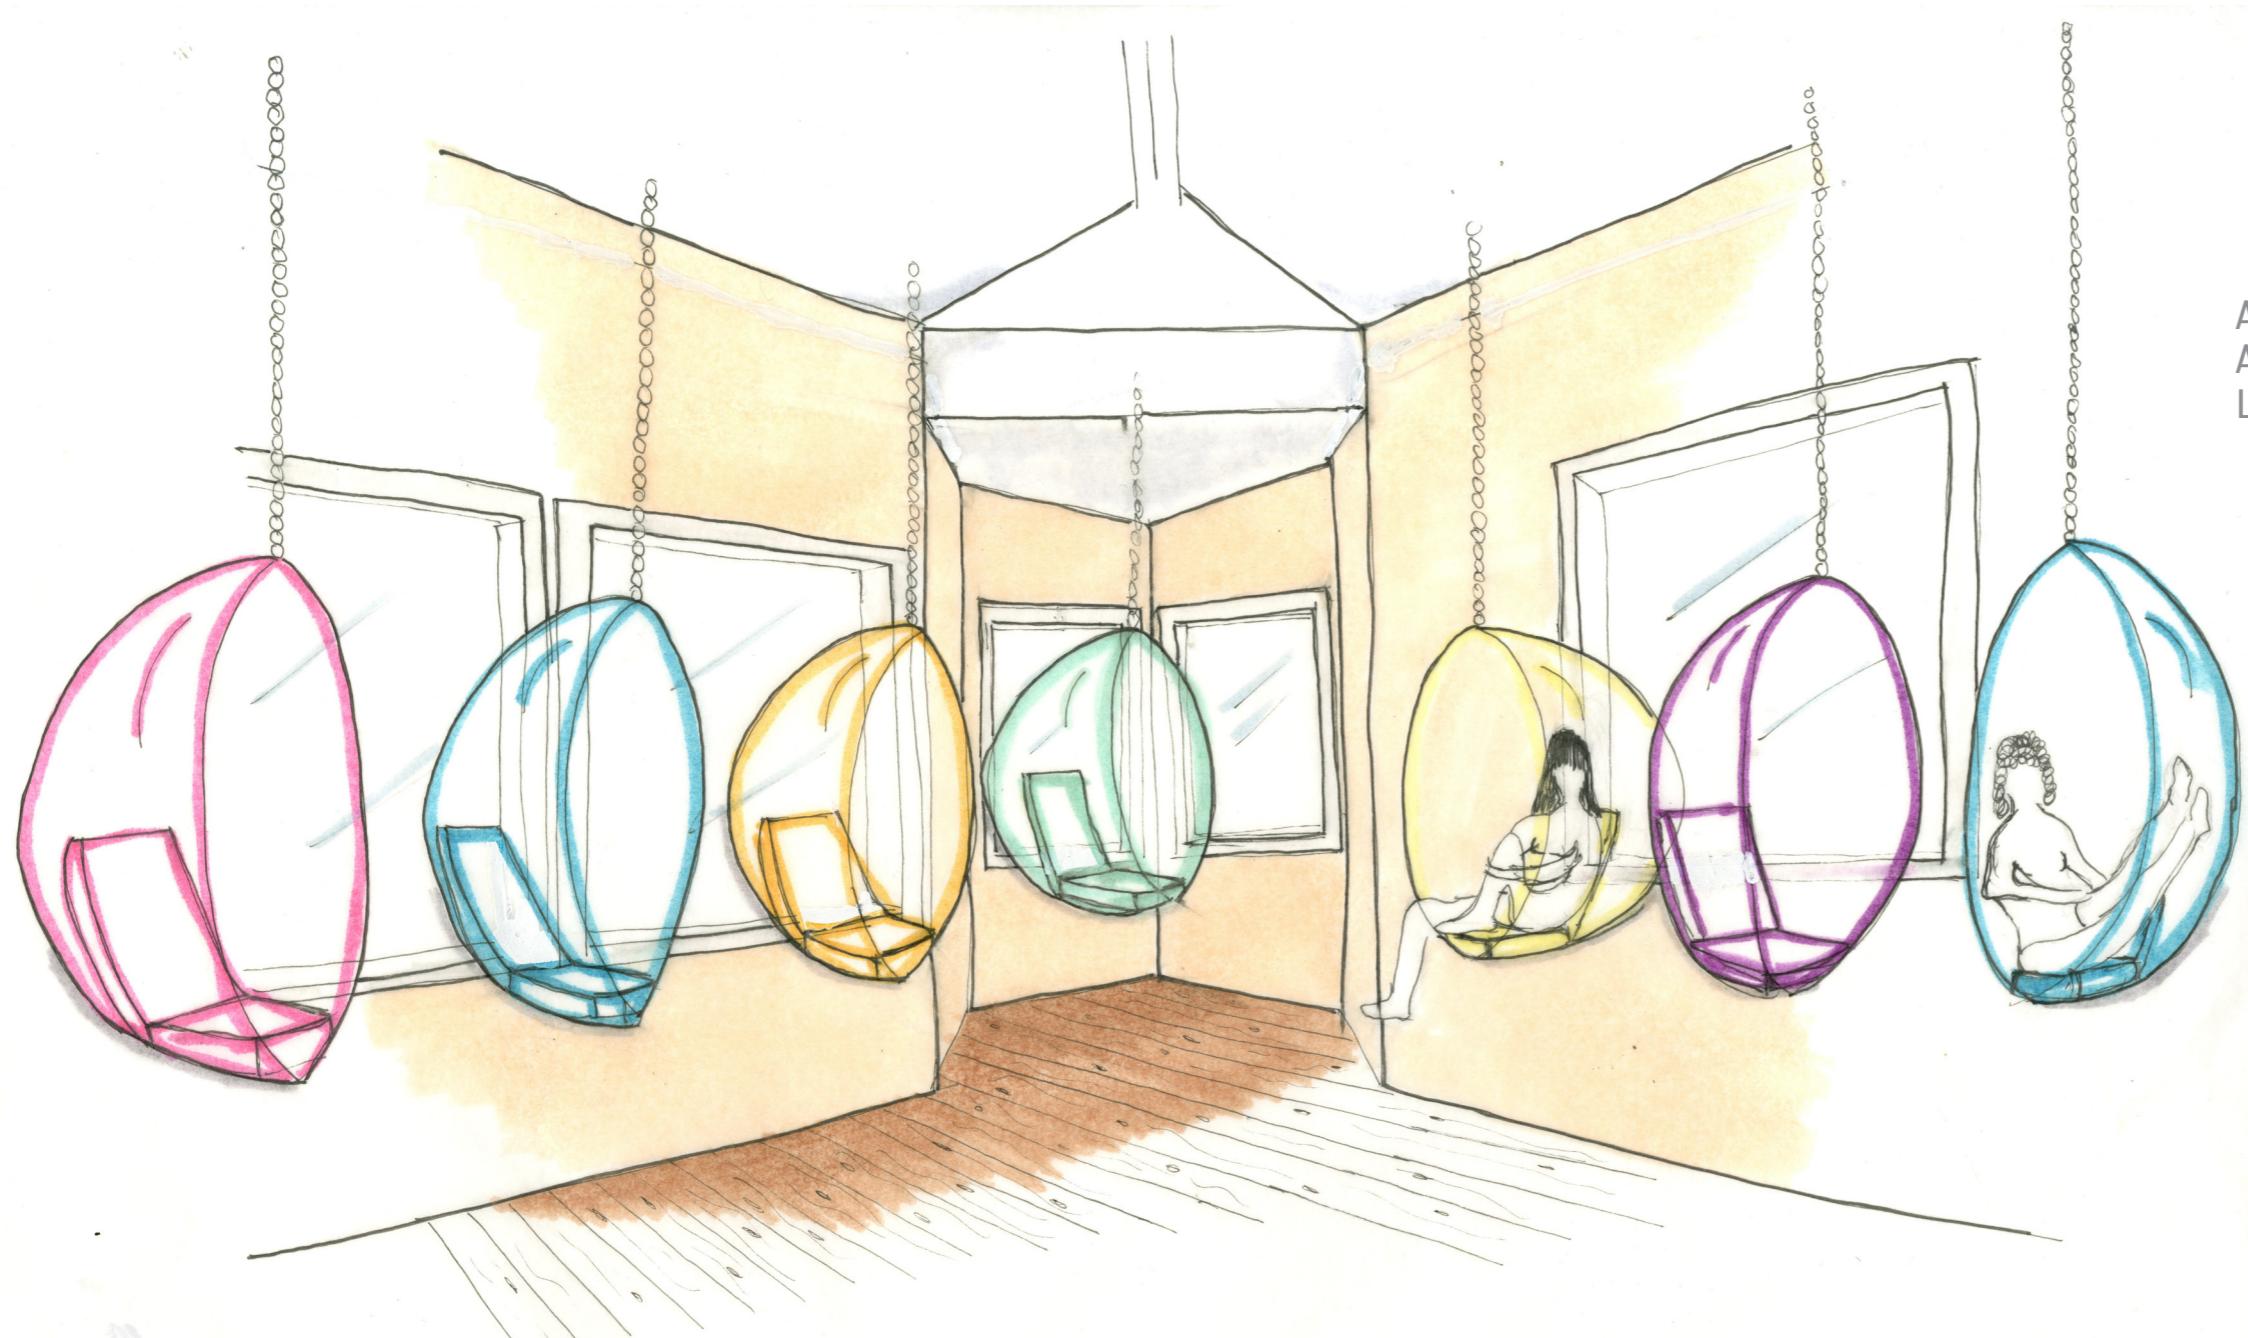


Adelta Eero  
Aarnio Bubble  
Lounge Chair



14:Sigt plan

PROJECT 1 : Surf club  
Dollymount Renovation  
June Therèse M Haugland

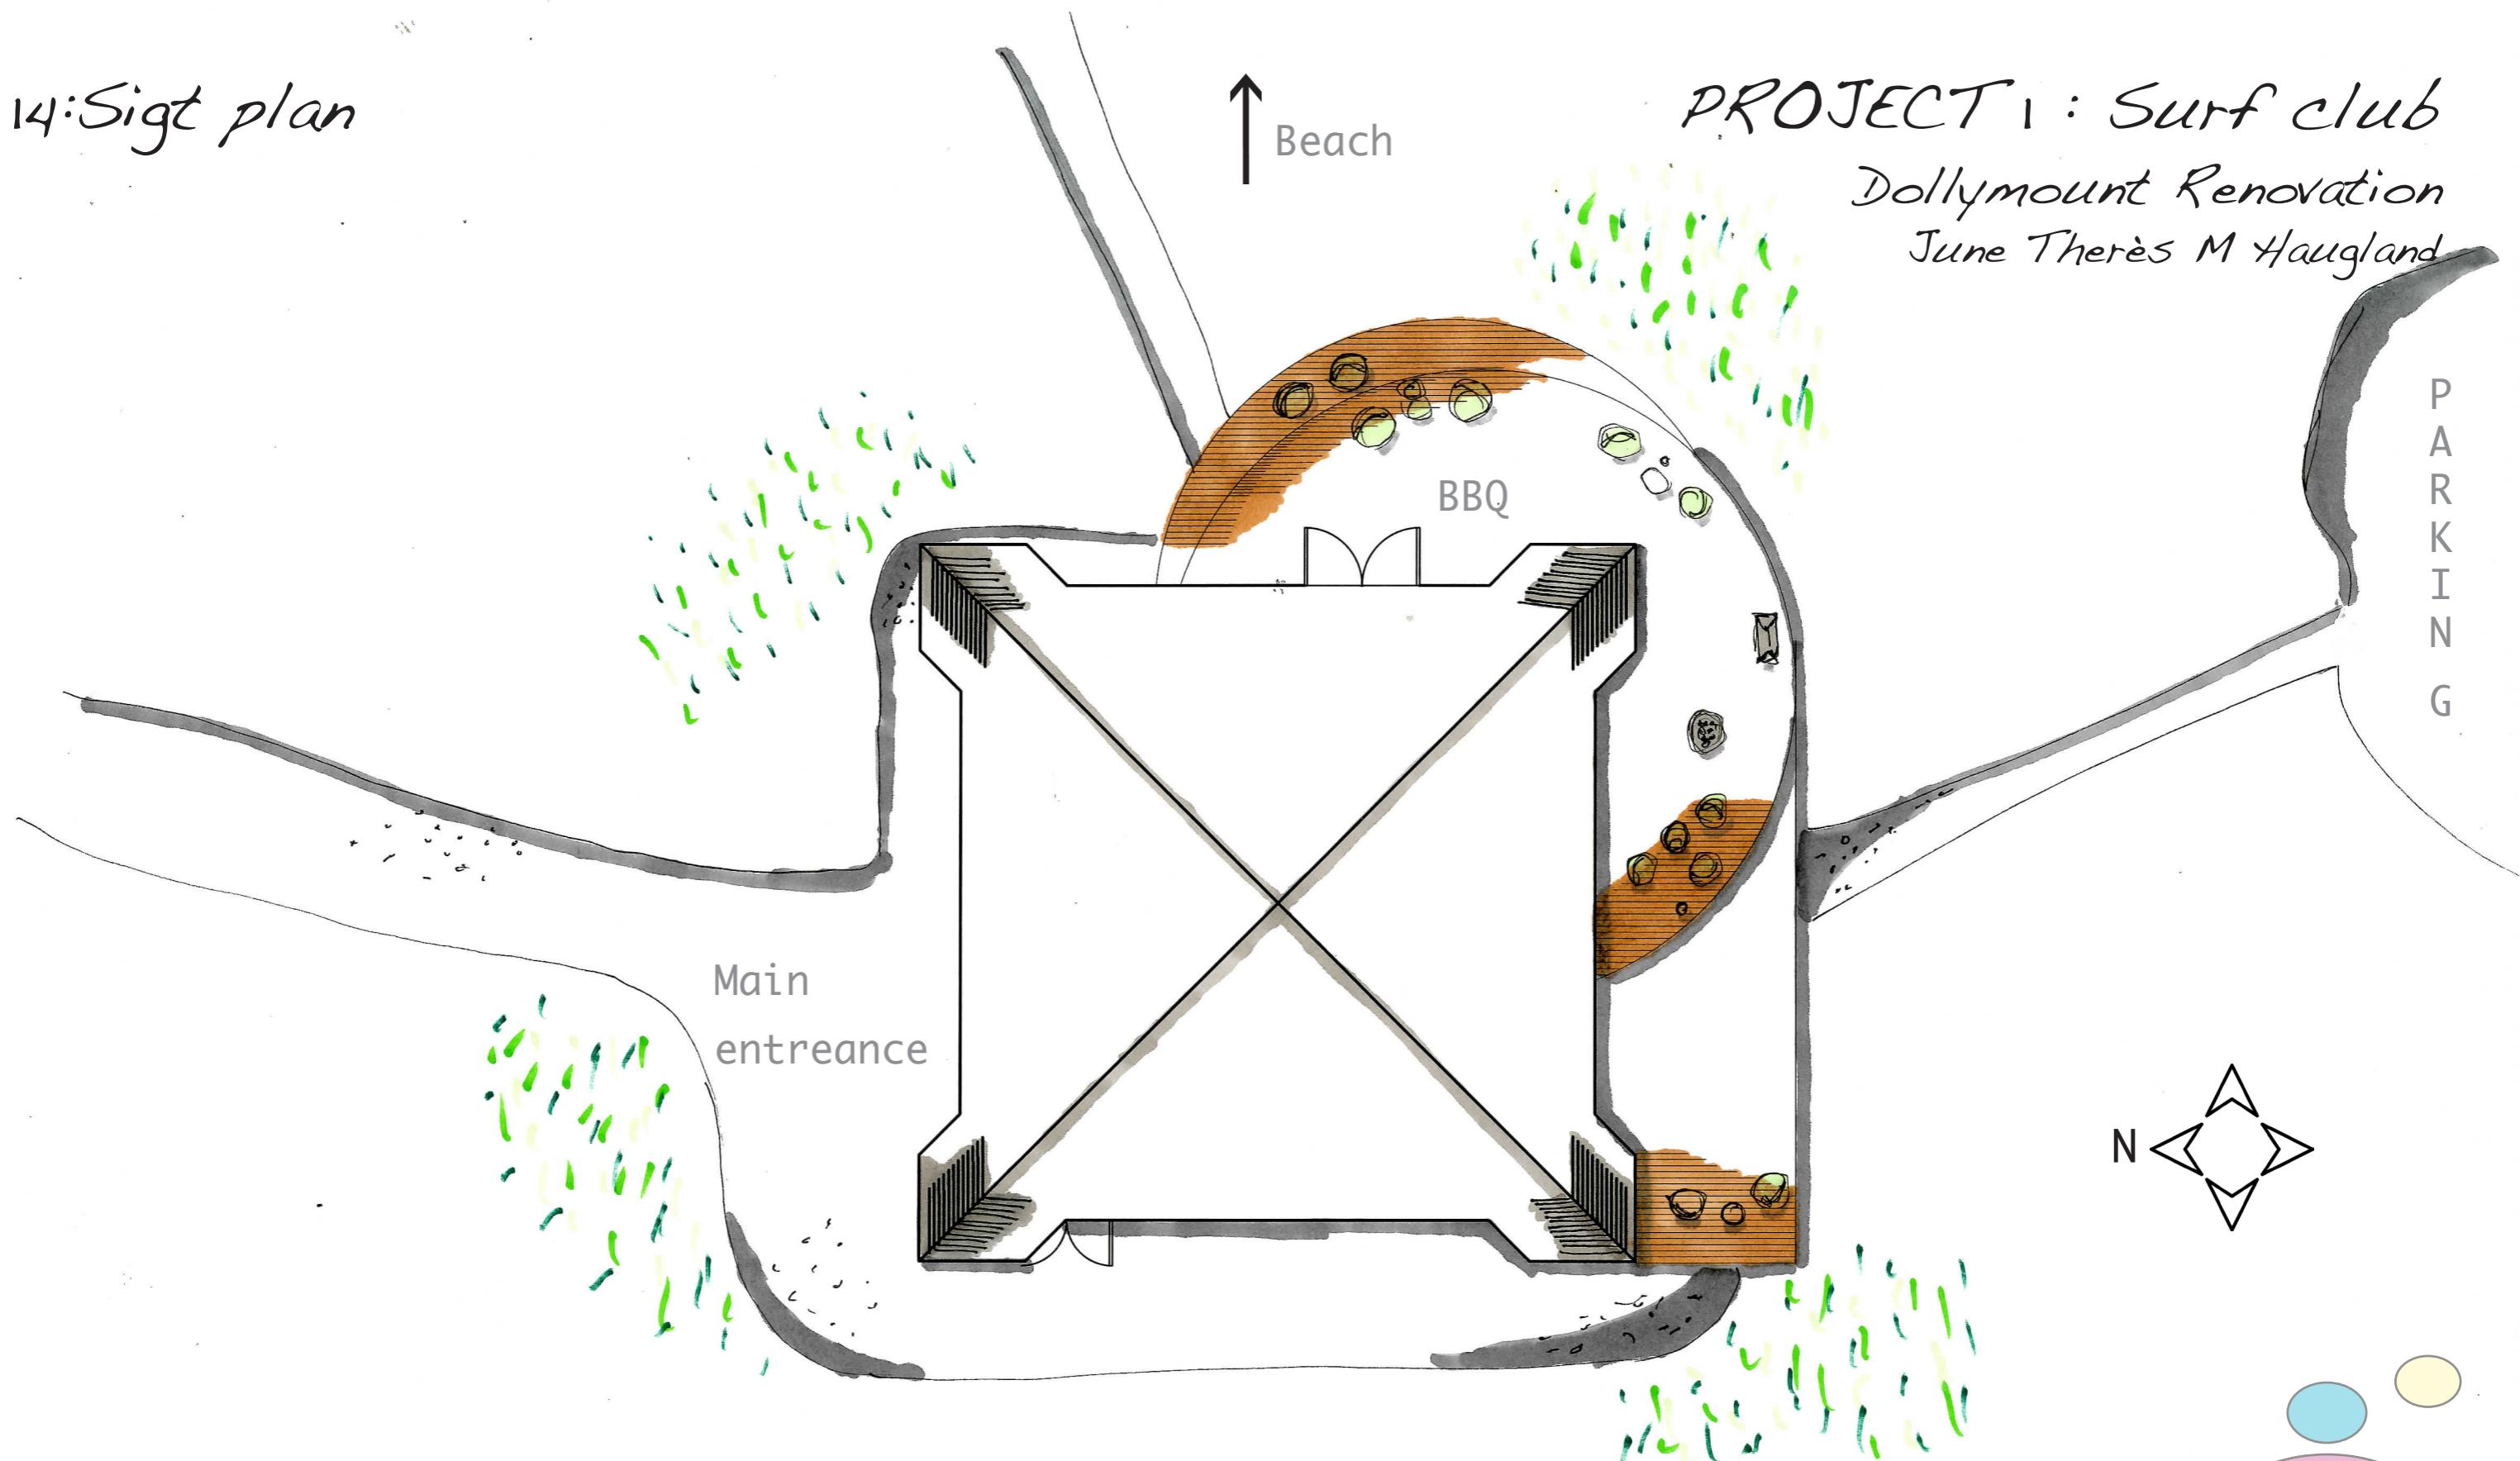


BUBBLES!  
16.10.2012  
Studnr: 2831878


# 15: Details

PROJECT 1 : Surf club  
Dollymount Renovation  
June Therèse M Haugland


Sitting bubble for 5-7 persons.

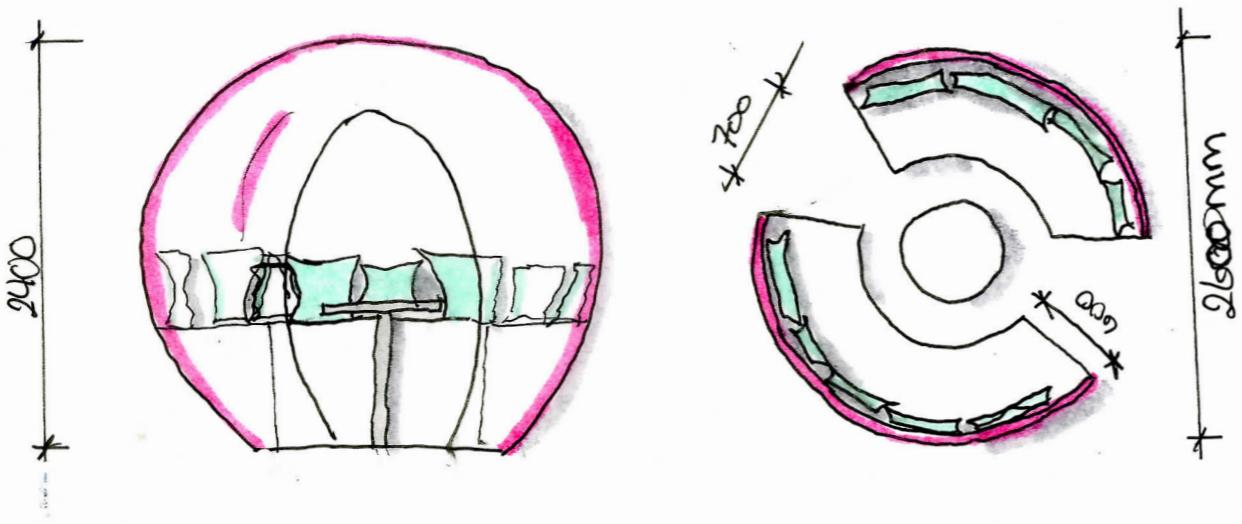


Cafè/ Ice krem bar

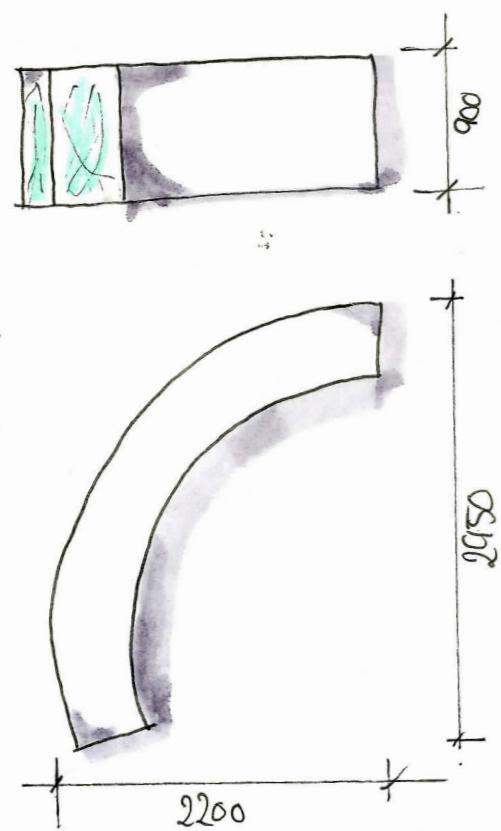

Reception

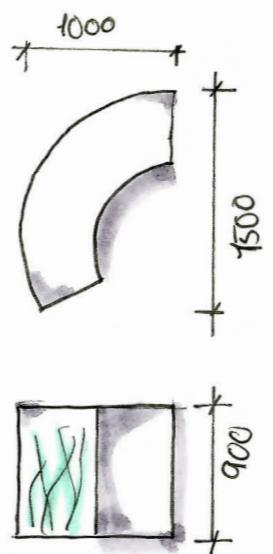


Glass wall with the stairs

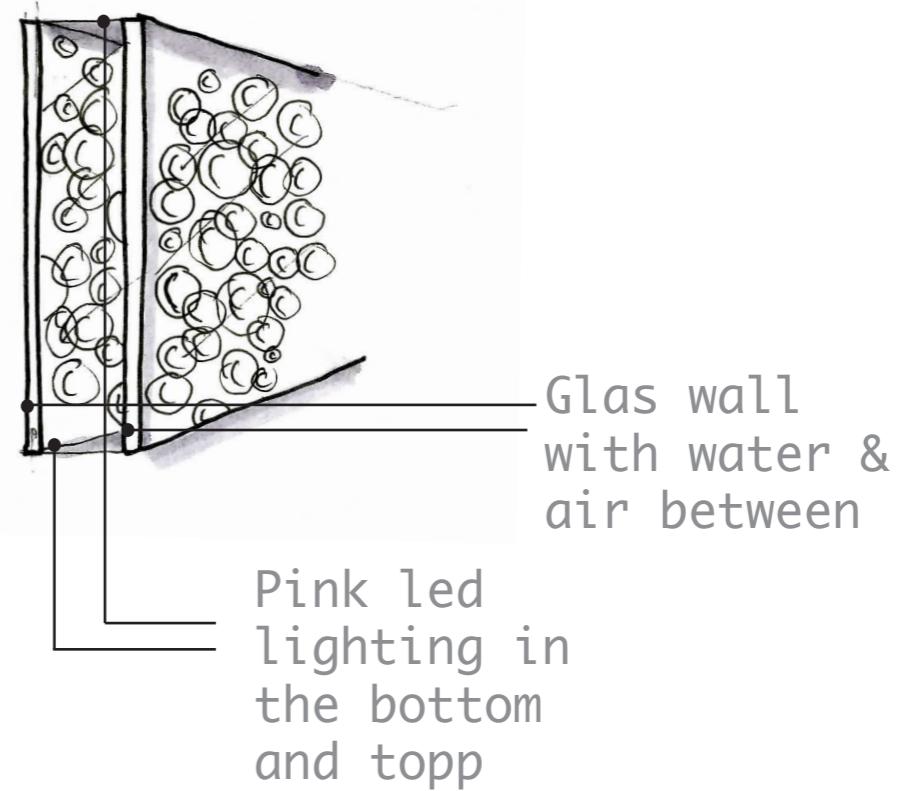


# 16. Materials


PROJECT 1 : Surf club  
Dollymount Renovation  
June Therèse M Haugland

 


NSC S 0510 Y60R  
Wall paint

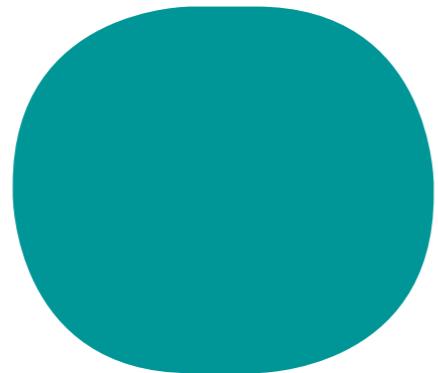


NSC S 2060 R50G  
Paint color in the  
window sitting

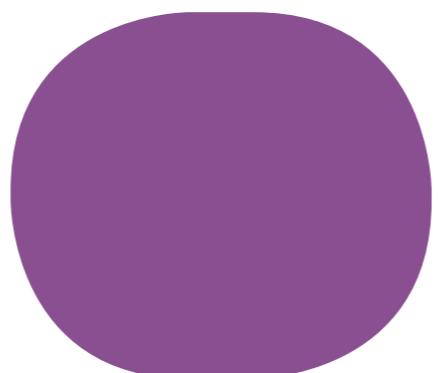

NSC S 3050 R50G  
Paint color in the  
window sitting

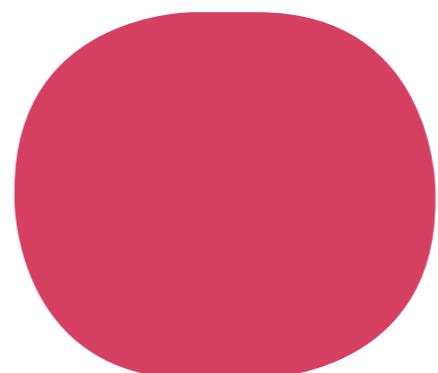


NSC S 1070 R10B  
Paint color in the  
window sitting

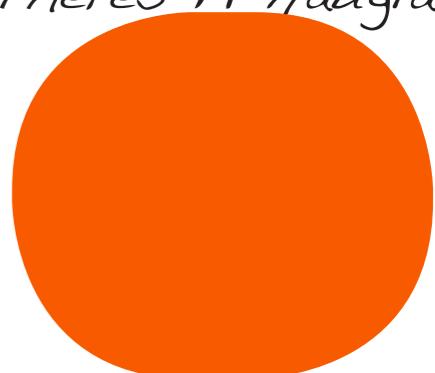


NSC S 0585 Y60R  
Paint color in the  
window sitting



Ceramic tiles  
Leather Beige mat  
Wall in changing  
room

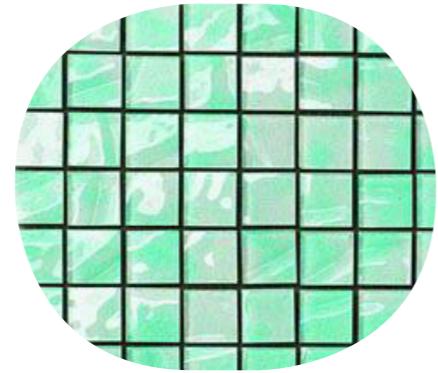

Anice Mosaici Musiva  
Plus  
Showerwall changing  
room men & toilet

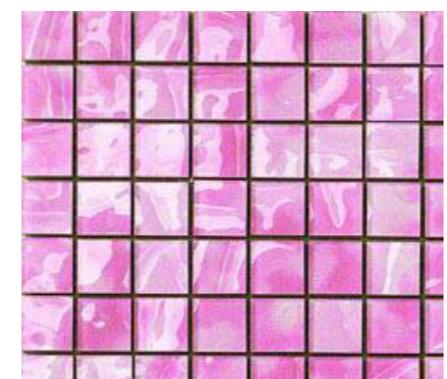

Rosso Vino Mosaici  
Musiva Plus  
Shower wall chanign  
room women & toilet




Geolite  
Beige grip nat  
Floor changing  
room



Floor tiles  
Rovere mat  
Ground floor




Formica Limed  
Strand Surfaces  
reception & cafè

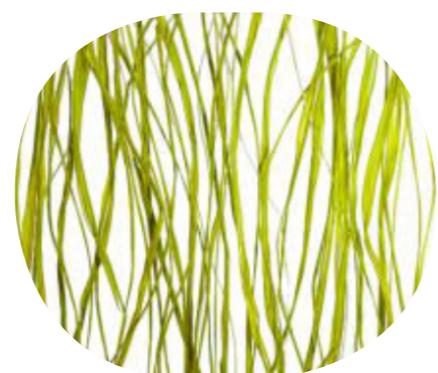

3Form seaweed  
glass + white out  
Front reception,  
cafè & dørs



Fiberglass  
Pastilli chair

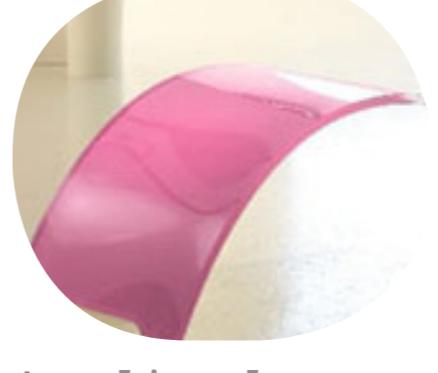

Acrylic glass  
Sitting bobble &  
Adelta Eero Aarnio  
Bubble Lounge Chair




# 17: Materials


PROJECT 1 : Surf club  
Dollymount Renovation  
June Therèse M Haugland




Parquet 1 strip  
Oak  
First floor

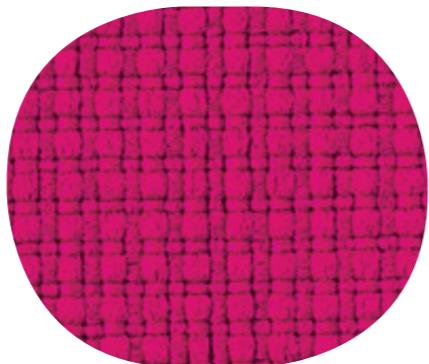

Urban Plus Cos-  
mopolitan  
Textil for  
chairs and benc

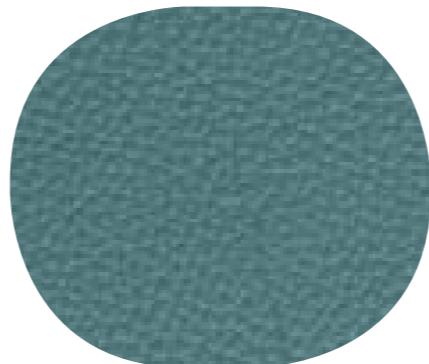


ELMONORDICL 78043  
Lather barstol

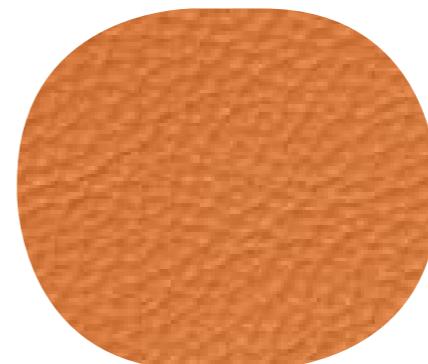


ELMONORDIC 54372  
Leather barstol




ELMONORDIC 04370  
Leather barsol

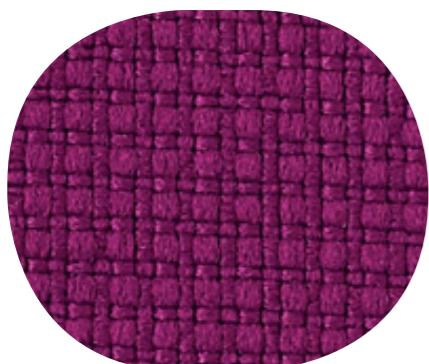

Intervene Tex-  
ture YW211  
Textile for  
chairs and bench

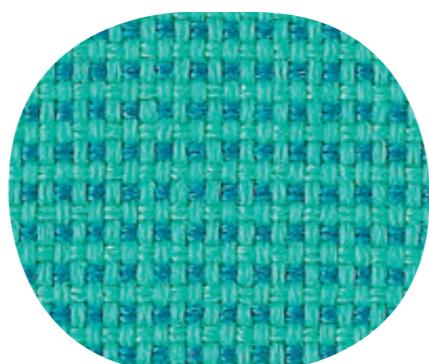


Château Plus  
Foix  
Textile for  
chairs and benc

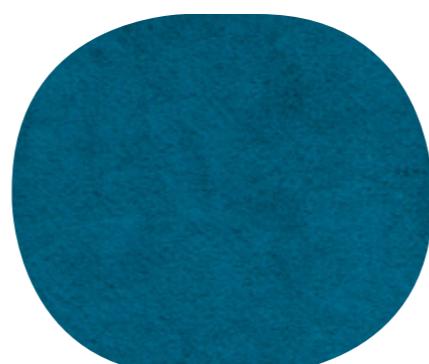

Velvetine Plus  
Ocelot  
Textile for  
chairs and benc



Blazer Ashville  
Textile for  
chairs and bench

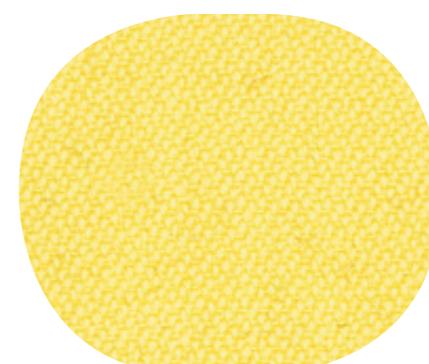


Oxygen Fresh  
Textile for  
chairs and bench



# 19: Material list

# PROJECT 1 : Surf club Dollymount Renovation June Therèse M Haugland

3. Paint	Window sitting	NCS S 3050 Y50B		
4. Paint	Window sitting	NCS S 1070 R10B		
5. Paint	Window sitting	NCS S 0585 Y60 R		
6. Tiles	Wall In the changing room	Ceramic tiles 0130065 Leather Beige mate 250x425x10mm	<a href="http://www.hoganes.no">www.hoganes.no</a>	
7. Tiles	Wall in the shower changing room men	S100506 Anice Mosaici Musiva Plus 22x22x10mm	<a href="http://www.hoganes.no">www.hoganes.no</a>	
8. Tiles	Wall in the shower changing room men	S100565 Rosso Vino Mosaici Musiva Plus 22x22x10mm	<a href="http://www.hoganes.no">www.hoganes.no</a>	
9. Tiles	Floor in changingroom	0140021 Beige mate, Grip Natural 400x803x10,5mm	<a href="http://www.hoganes.no">www.hoganes.no</a>	

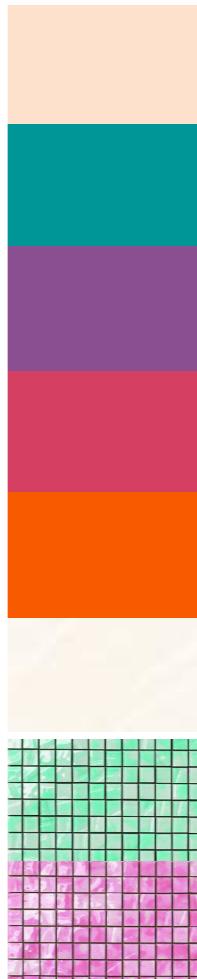

# 20:Material list

# PROJECT 1 : Surf club Dollymount Renovation June Therèse M Haugland

ITEM	LOCATION	SPECIFICATION	SUPPLIER	SAMPLE FOR CLIENT
9. Tiles	Floor in changingroom	0140021 Beige mate, Grip Natural 400x803x10,5mm	<a href="http://www.hoganes.no">www.hoganes.no</a>	
10. Tiles	Floor in entrance, reception, manager & surfboard storage	Chalet 0040222 Rovere mate 195x800x9mm	<a href="http://www.hoganes.no">www.hoganes.no</a>	
11. High Pressure Laminate	Topp surface reception & Cafè/ Ice krem bar	Limed Strand F6305	<a href="http://www.fomica.com">www.fomica.com</a>	
12. 3form resin	Front surfacereception, Cafè/ Ice krem bar & all doors	Seaweed glass+ white out	<a href="http://www.3form.eu">www.3form.eu</a>	
13. Fibreglass	Pastilli chair			
14. Acrylic glass	Sitting bobble & Adelta Eero Aarnio Bubble Lounge Chair			
15. Parquet	Parquet flooring first floor	New Classic Galway, Oak 1 strip 90x120x220mm	<a href="http://www.gulvspesialisten.no">www.gulvspesialisten.no</a>	
16. Textil	Textil for benc & pillows	Urban Plus Cosmopolitan Product code: YN203 Application Seating Composition 100% Recycled flame retardant polyester Martindale 100 000	<a href="http://www.camirafabrics.com">www.camirafabrics.com</a>	



# 21:Material list

# PROJECT 1 : Surf club Dollymount Renovation June Therèse M Haugland

ITEM	LOCATION	SPECIFICATION	SUPPLIER	SAMPLE FOR CLIENT
16. Textil	Textil for benc & pillows	Urban Plus Cosmopolitan Product code: YN203 Application Seating Composition 100% Recycled flame retardant polyester Martindale 100 000	<a href="http://www.camirafabrics.com">www.camirafabrics.com</a>	
17. Textil	Leather for barstols	Grain leather Elmonordic No: 78043 NCS S 6020 B70G Pantone:5477C	<a href="http://www.elmonleather.com">www.elmonleather.com</a>	
18. Textil	Leather for barstols	Grain leather Elmonordic No: 54372 NCS S: 3050 Y50R Pantone: 471C	<a href="http://www.elmonleather.com">www.elmonleather.com</a>	
19. Textil	Leather for barstols	Grain leather Elmonordic No: 04370 NCS S 2060 Y20R Pantone: 7411C	<a href="http://www.elmonleather.com">www.elmonleather.com</a>	
20. Textil	Textil for benc & pillows	Intervene Texture Product code: YW211 Application: Seating Composition 100% Recycled flame retardant polyester Martindale 100 000	<a href="http://www.camirafabrics.com">www.camirafabrics.com</a>	
21. Textil	Textil for benc & pillows	Château Plus Foix Product code: CSP30 Application: Seating Composition 100% Prefentex Martindale 100 000	<a href="http://www.camirafabrics.com">www.camirafabrics.com</a>	
22. Textil	Textil for benc & pillows	Velvetine Plus Ocelot Product code: VII04 Application: Seating Composition: Surface: 100% polyamide Substrate: 65% Polyester 35% cotton Martindale 100 000	<a href="http://www.camirafabrics.com">www.camirafabrics.com</a>	
23. Textil	Textil for benc & pillows	Blazer Ashville Product code: CUZ50 Application: Seating Composition: 100% Pure New Wool Martindale 50 000	<a href="http://www.camirafabrics.com">www.camirafabrics.com</a>	

